



GENERAL NOTES

ALL ELEVATION ARE TAKEN FROM BASE LINE ELEVATION OF LEVEL PENTHOUSE(ROOF)= 140.73'

KEY PLAN

A

B

ABBREVIATIONS

ELECTRICAL

PLUMBING

MECHANICAL

FIRE PROTECTION

Revision/Issue

Date

Firm Name and Address

Project Name and Address

1109 CONGRESS STREET

1109 CONGRESS STREET, NE
WASHINGTON, DC 20002

Project Area

PENTHOUSE(ROOF)
OH CMP PLAN

Original Date

09/25/2025

Plot Date


09/26/2025

Scale

1/4"=1'-0"

Sheet

PH(ROOF)_OH_CMP

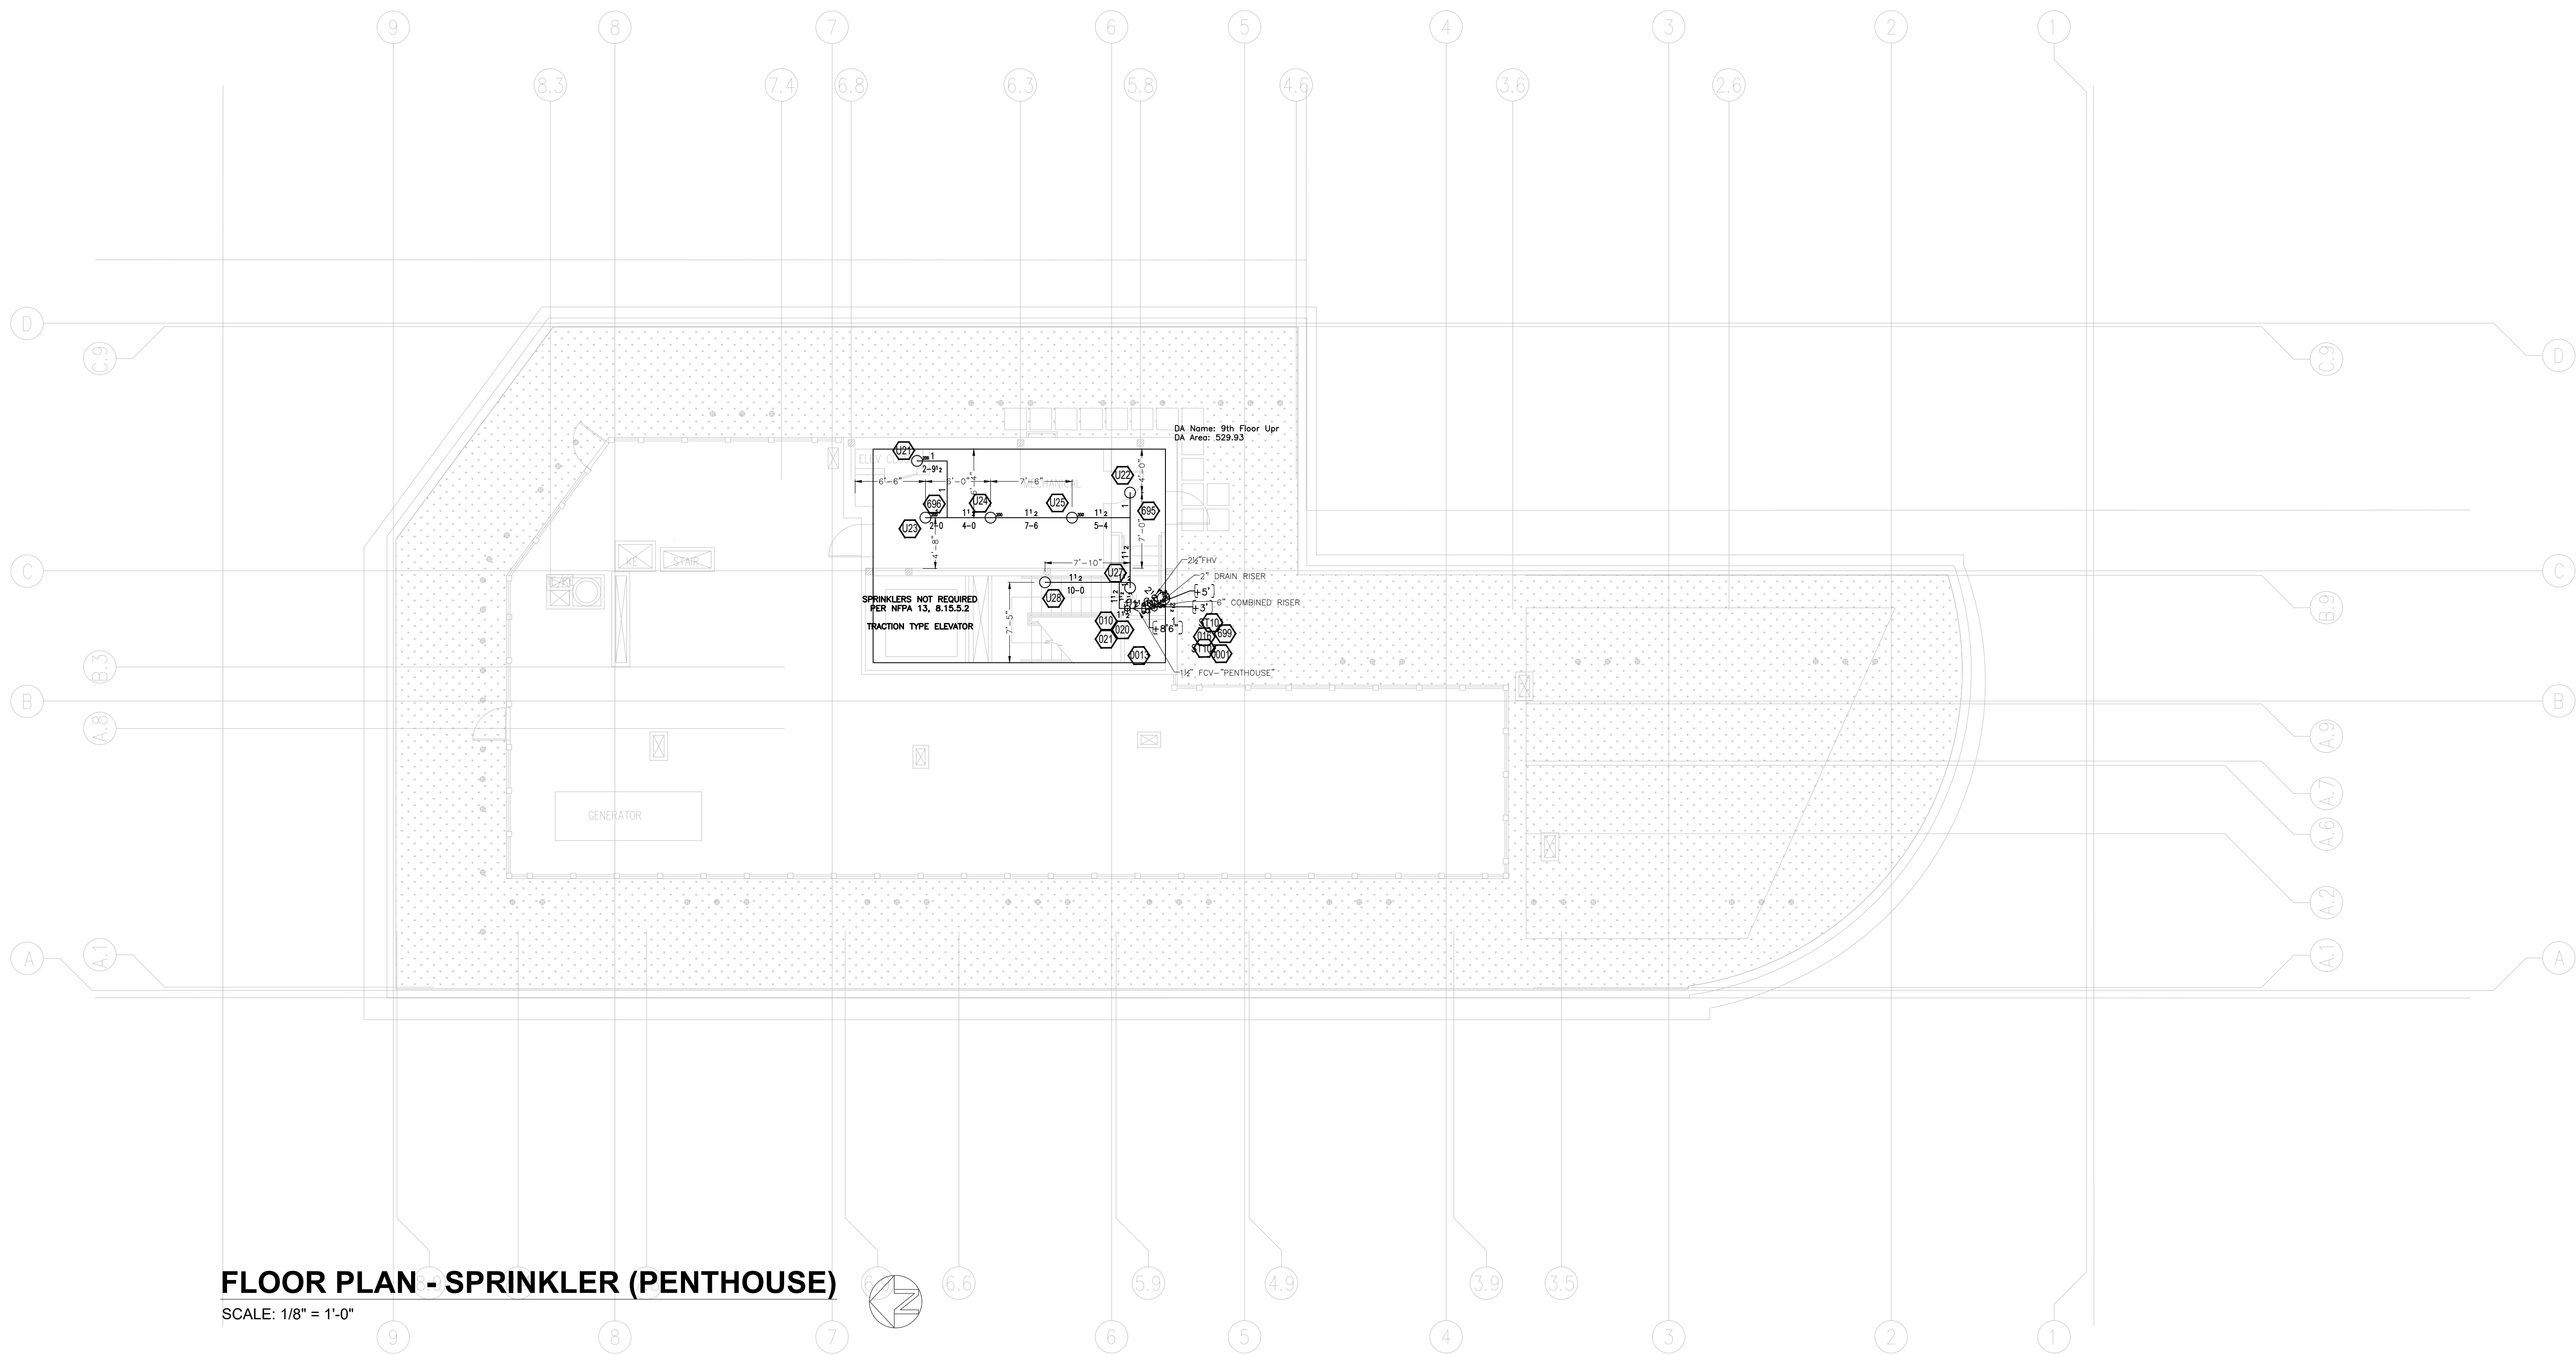

FLOOR PLAN - SPRINKLER (PENTHOUSE)
SCALE: 1/8" = 1'-0"



WASHINGTON
SPRINKLER


12067 CADET CT.,
MANASSAS VA 20109
T 571.229.9058, F 703.997.0577

WWW.WASHINGTONSPRINKLER.COM

PROJECT NAME

1109 CONGRESS ST. NE
WASHINGTON DC 20015

ENGINEERING SEAL

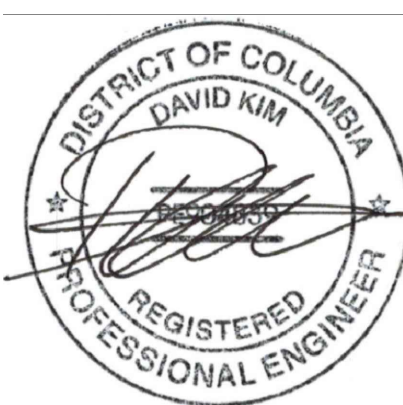

SPRINKLER LEGEND										
SYMBOL	TYPE	K	RESP	ORF.	TEMP	MANUF.	SPRKL. FINISH	ESCUT. FINISH	MODEL	SN
●	STANDARD PENDENT	5.6	DR	1/2	155	RELIABLE	CHROME	CHROME	F1FR56	RA1414
●	RESIDENTIAL PENDENT	4.9	DR	1/2	100	RELIABLE	WHITE	WHITE	F1RES49	R3516
●	INTERMEDIATE TEMP. RESIDENTIAL PENDENT	4.9	DR	1/2	175	RELIABLE	WHITE	WHITE	F1RES49	R3516
●	RESIDENTIAL SIDEWALL	4.4	DR	1/2	100	RELIABLE	WHITE	WHITE	F1RES44	R3531
●	INTERMEDIATE TEMP. RESIDENTIAL SIDEWALL	4.4	DR	1/2	175	RELIABLE	WHITE	WHITE	F1RES44	R3531
●	HALLWAY PENDENT	5.6	DR	1/2	155	RELIABLE	WHITE	WHITE	L756	RA5814
○	STANDARD UPRIGHT	5.6	DR	1/2	155	RELIABLE	BRASS	N/A	F1FR56	RA1423
○	STANDARD L. TEMP. UPRIGHT	5.6	DR	1/2	175	RELIABLE	BRASS	N/A	F1FR56	RA1423

SPRINKLER LEGEND										
SYMBOL	TYPE	K	RESP	ORF.	TEMP	MANUF.	SPRKL. FINISH	ESCUT. FINISH	MODEL	SN
●	DRY PENDENT	5.6	DR	1/2	155	RELIABLE	CHROME	CHROME	F3DR	R5714
●	HORIZONTAL SIDEWALL	5.6	DR	1/2	155	RELIABLE	CHROME	CHROME	F1FR56	RA1435
●	HORIZONTAL SIDEWALL	5.6	DR	1/2	155	RELIABLE	CHROME	CHROME	F3DR	R5734
TOTAL SPRINKLERS										

GENERAL LEGEND			
CEILING TYPE ABBREVIATION			
A	ACOUSTIC CEILING TILE		
B	GYPSUM BOARD		
C	OPEN TO SLAB		
PIPE DEPARTMENT CONNECTIONS			
1	PIPE DEPARTMENT CONNECTIONS		
2	BACKFLOW PREVENTION ASSEMBLY		
3	CHECK VALVE		
4	BUTTERFLY VALVE W/ TAMPER SWITCH		
5	WATERFLOW SWITCH		

DESIGNED BY	JM/DK	DATE	01-22-2025	WFPE NO.	DC5497
DRAWN BY	JM/RK			CLIENT NO.	
CHECKED BY	DK			SHEET NO.	
LICENSE NO.	DISTRICT OF COLUMBIA FIRE SPRINKLER CONTRACTOR LICENSE NO.1336				

LEGEND:

POWER

MS-S: MAIN SWITCHBOARD SOUTH

MS-N: MAIN SWITCHBOARD NORTH

CG ELECTRIC, INC.

EMPOWERING
BIM TECHNOLOGY


eng

REVISION SCHEDULE

REV.	DESCRIPTION	DATE

Is this the latest version?
SCAN ME

THIS DRAWING HAS BEEN REVIEWED AND APPROVED BY THE CLIENT

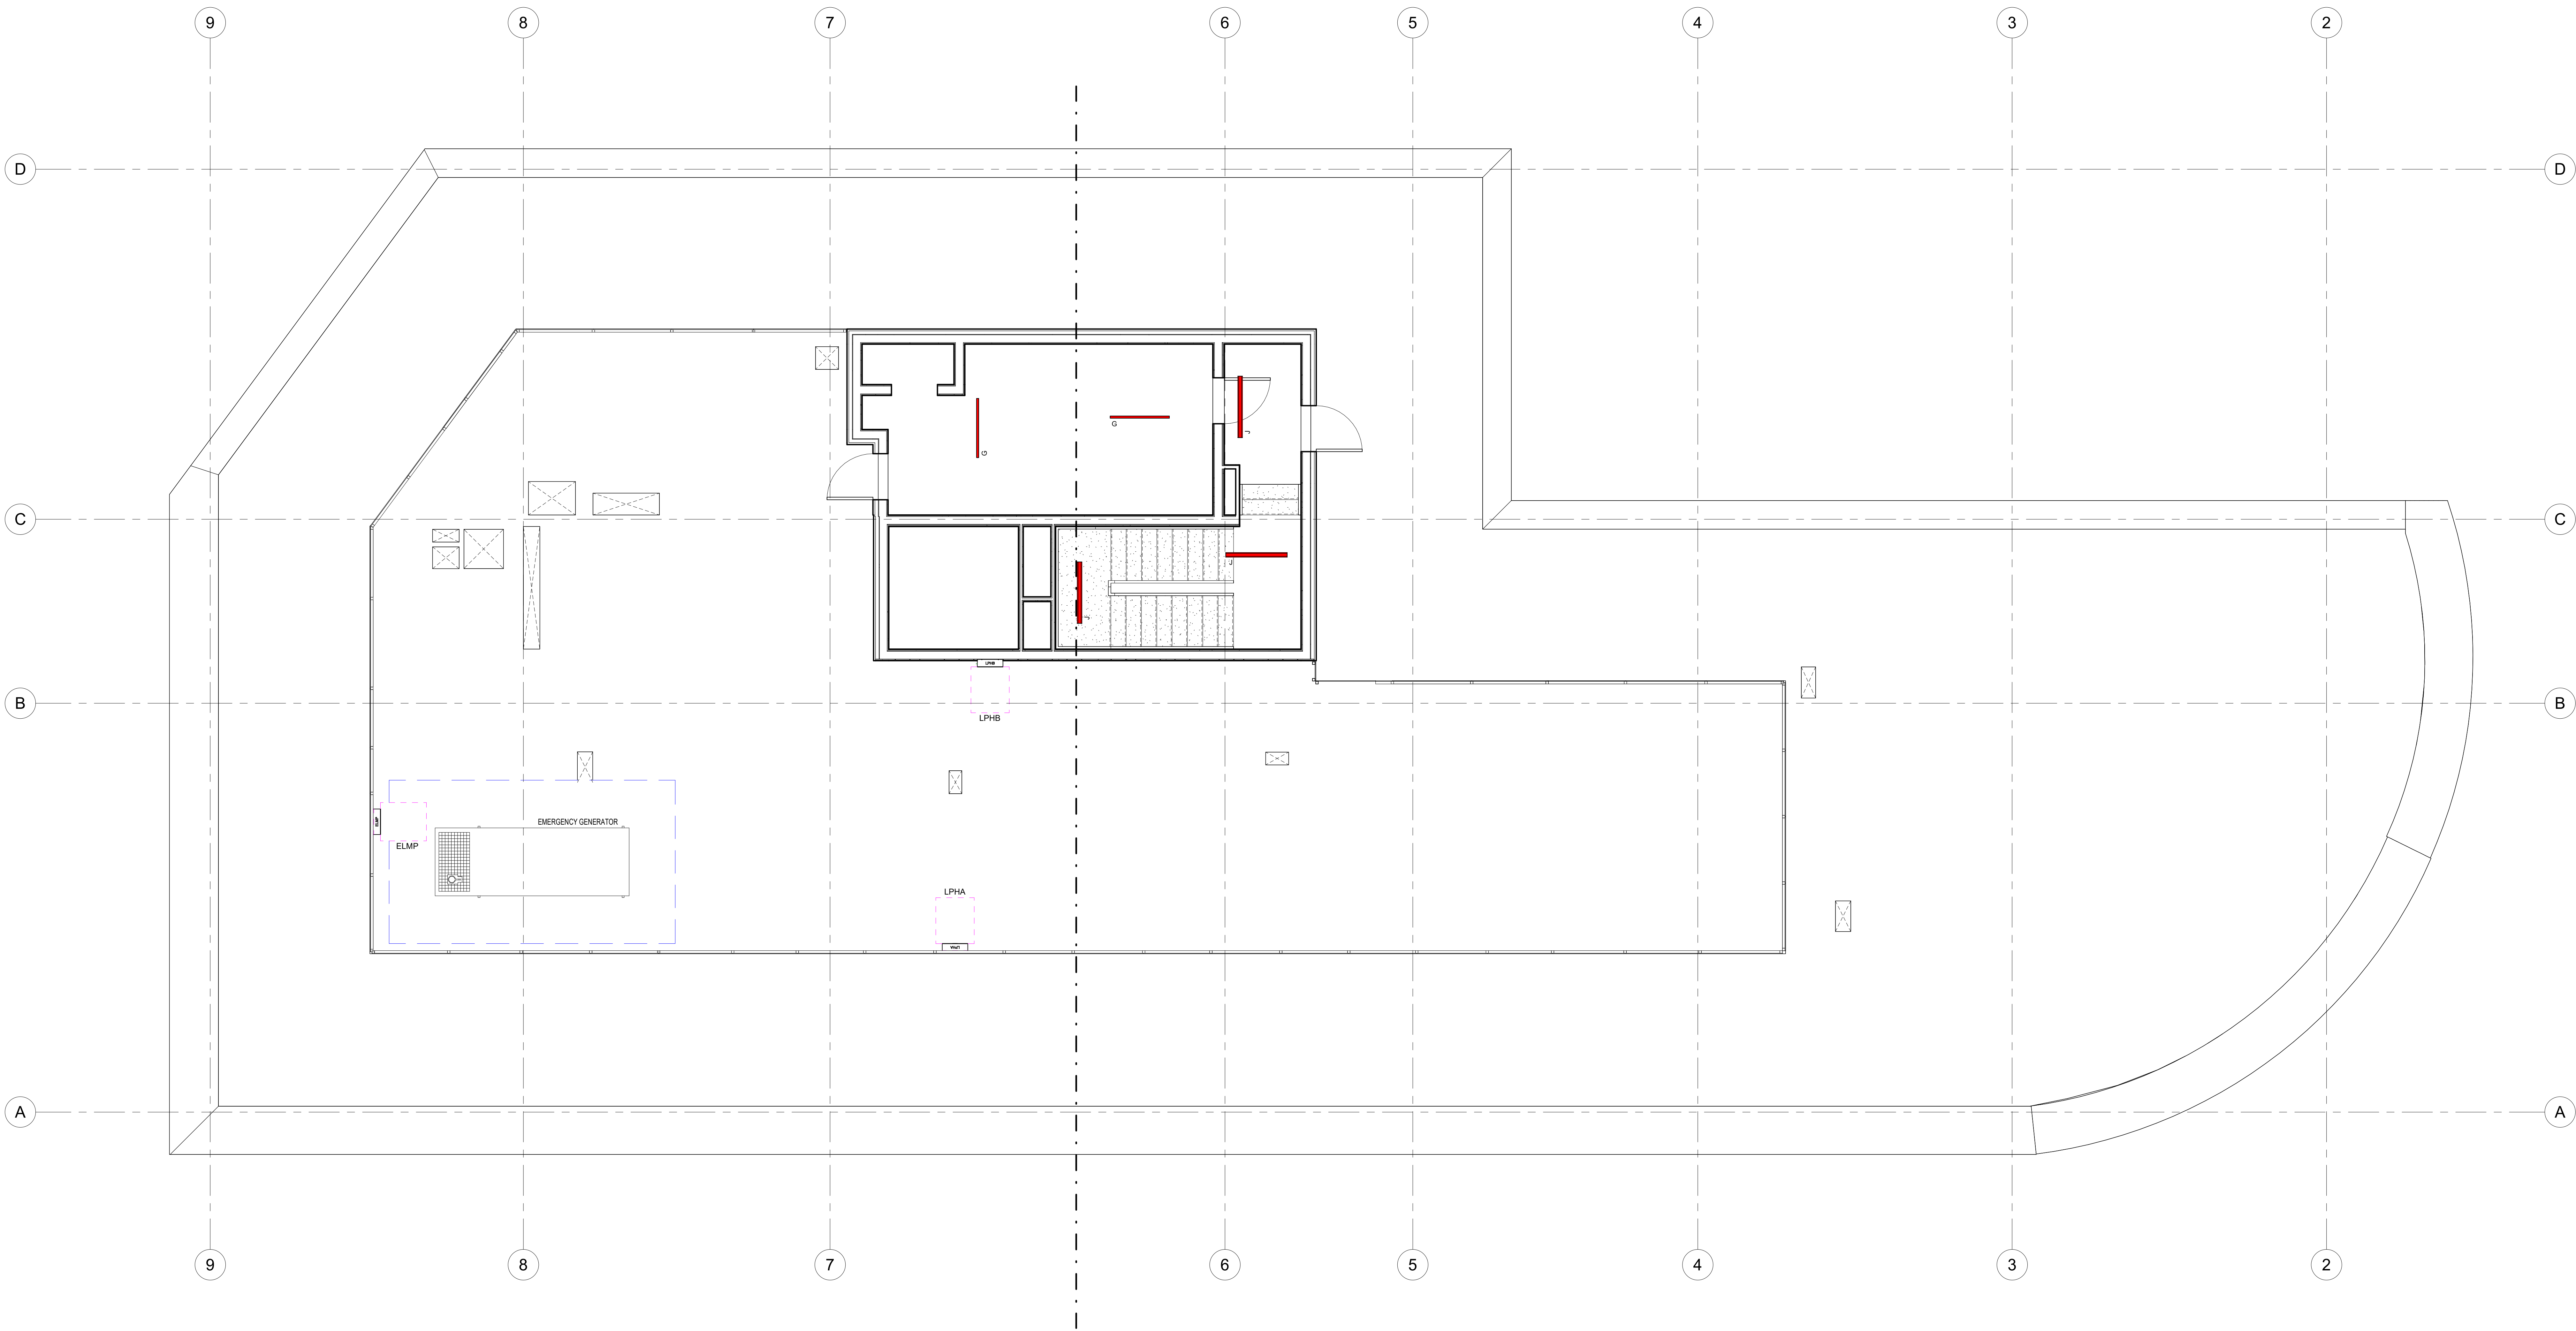

PROJECT NAME

1109 CONGRESS STREET NE
1109 Congress Street, NE
Washington, DC 20002

SHEET NAME

Penthouse Floor Overall

DRAWN BY: ENG


CHECKED BY: JB

DATE: 06/12/25

SCALE: As indicated


SHEET

E-310

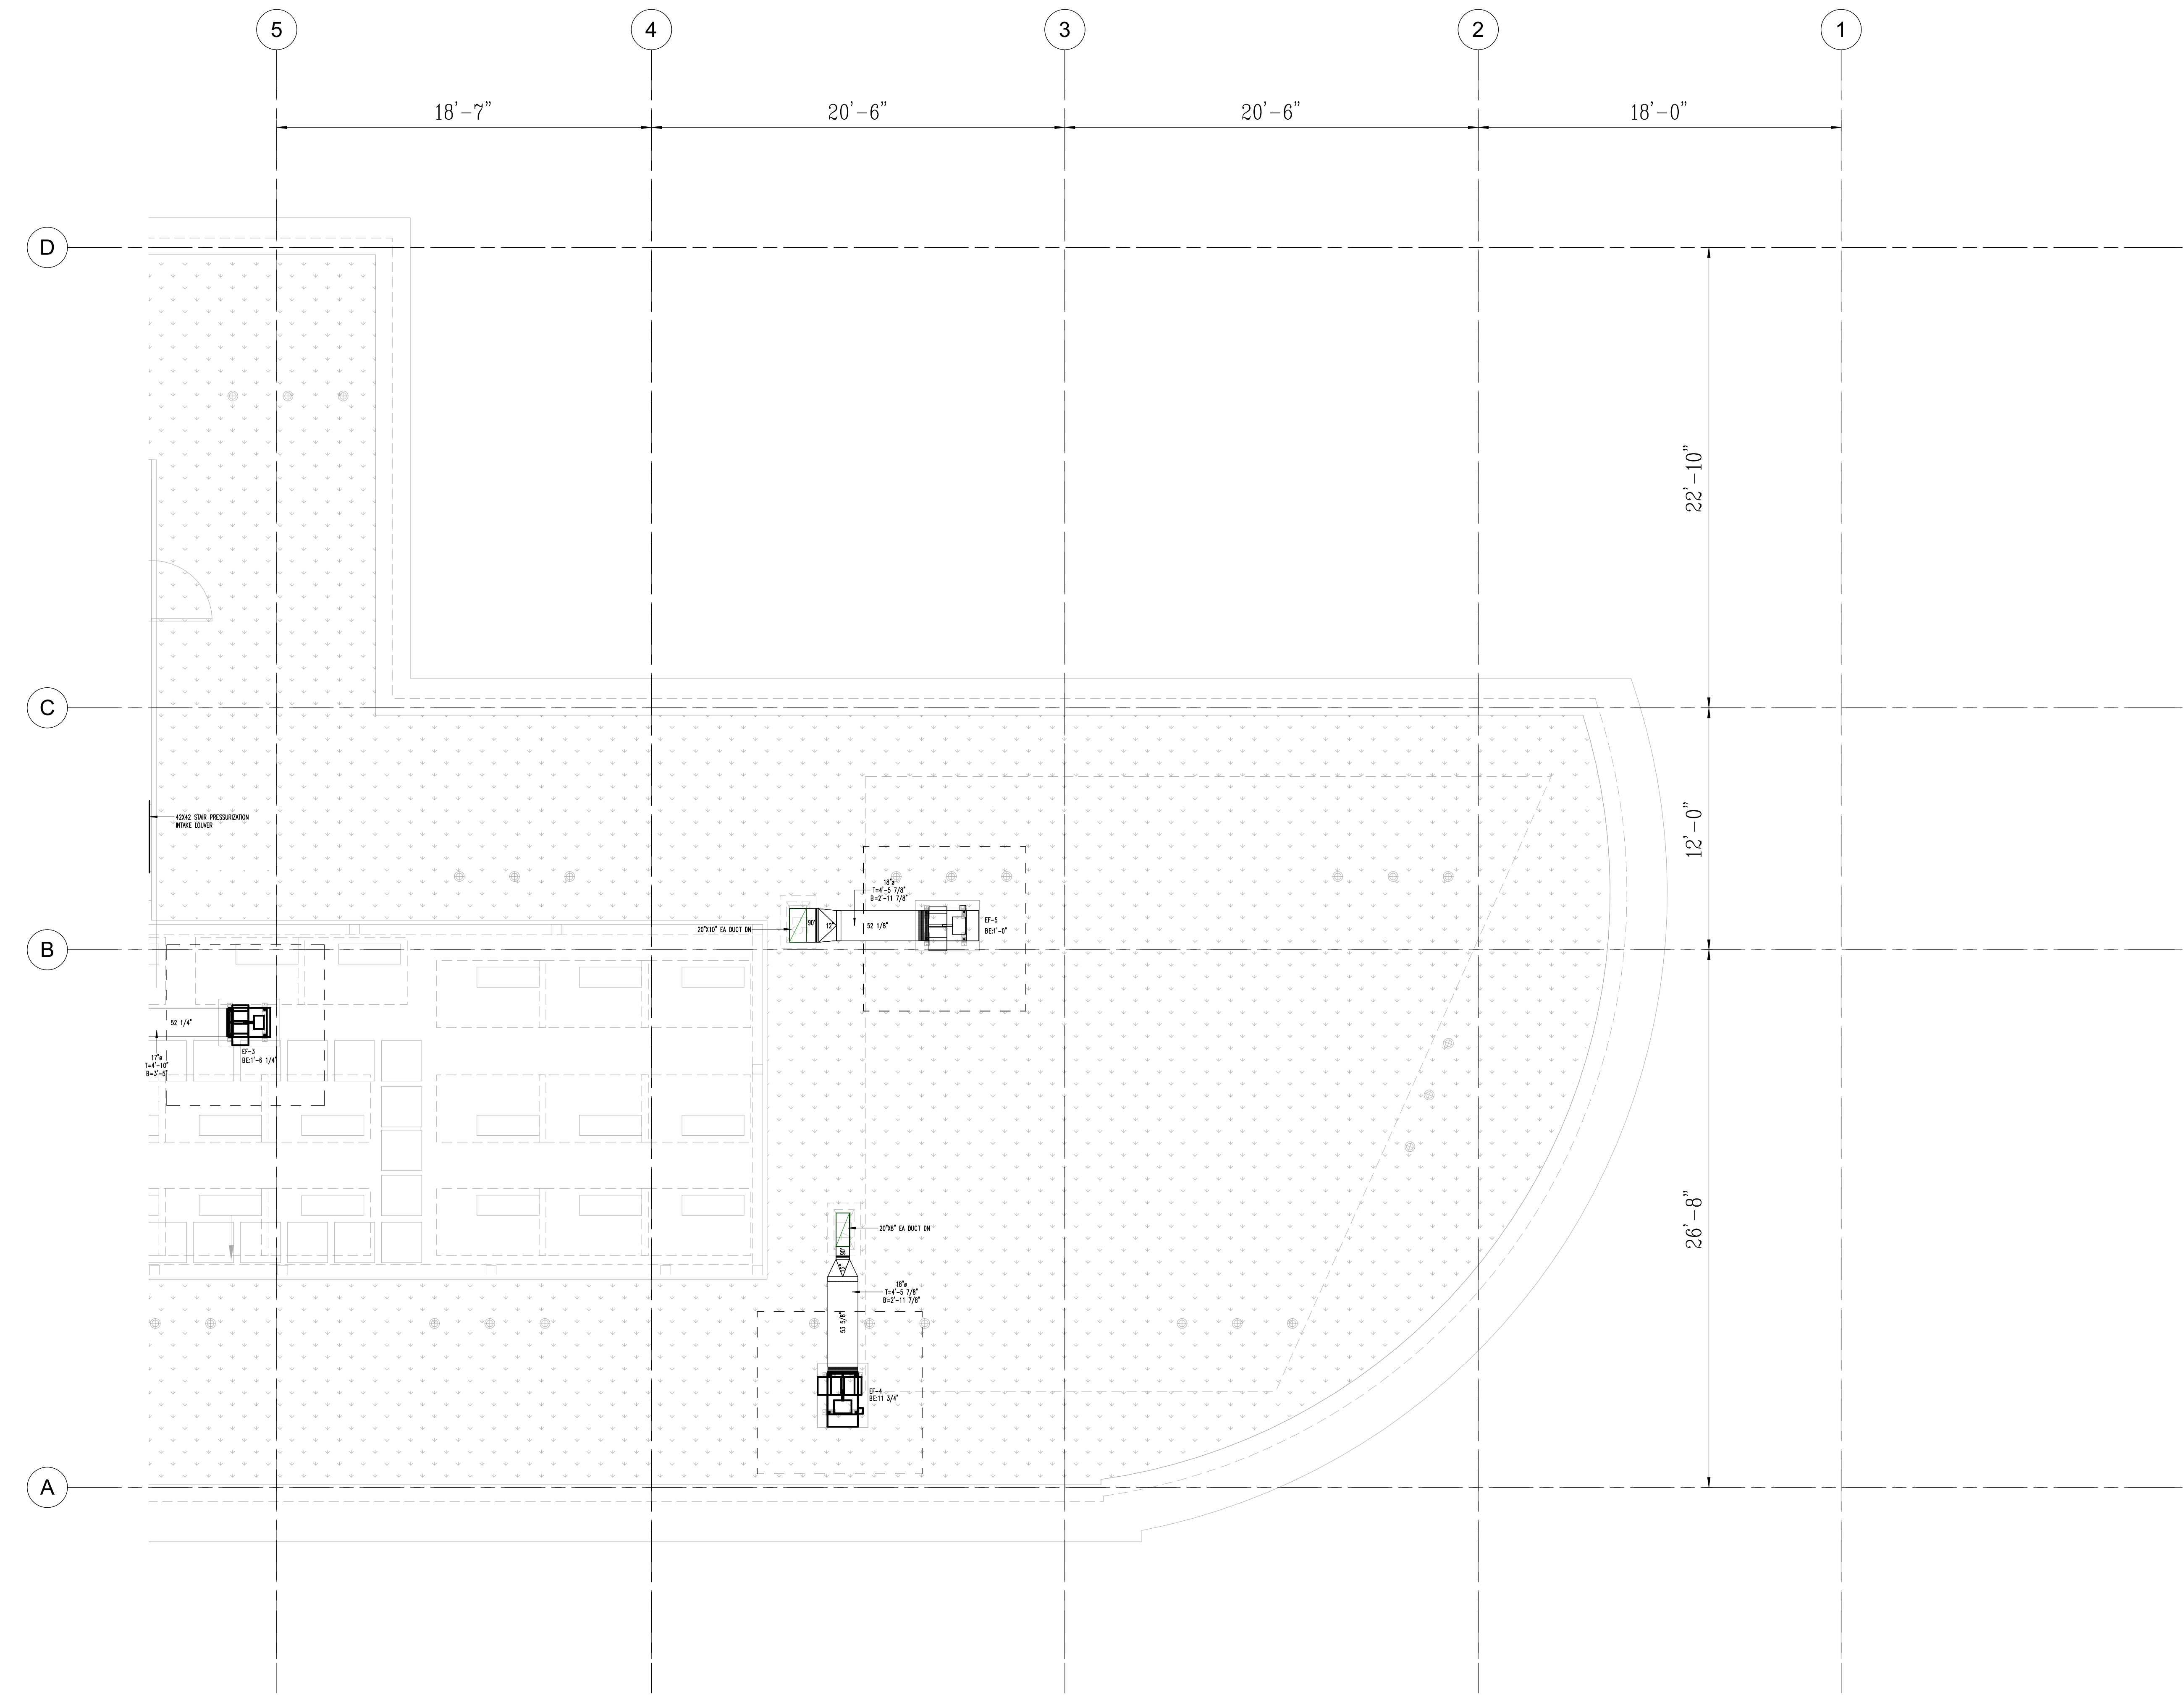

① 11-MAIN ROOF T.O.S.OH - AREA A
1/4" = 1'-0"

GENERAL NOTES
ALL ELEVATIONS ARE TAKEN FROM LEVEL - MAIN ROOF TOS=139.35'
ALL MECHANICAL EQUIPMENT ELEVATIONS ARE TAKEN FROM FFL

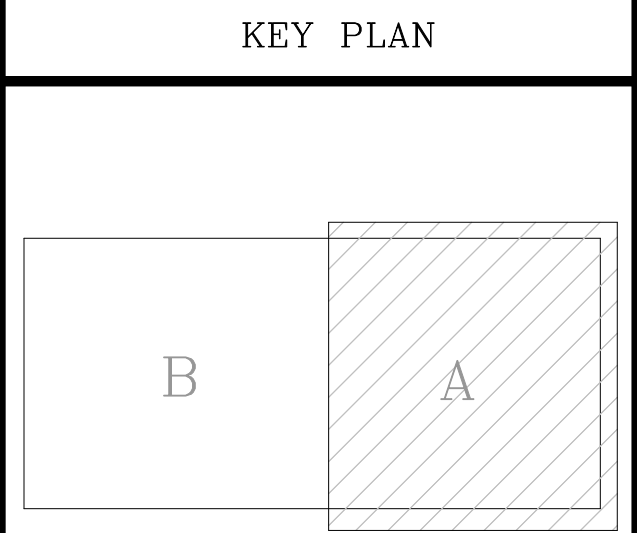


Updated as per comments	09/25/2025
For Review	08/06/2025
Revision/Issue	Date

Firm Name and Address


Project Name and Address
1109 CONGRESS STREET,NE
1109 CONGRESS STREET, NE
WASHINGTON, DC 20003

Project Area LEVEL- PH ROOF DUCT AREA A	Sheet SM-LPH-A-OH
Original Date 07/11/2025	Plot Date 09/25/2025
Scale 1/4"=1'-0"	

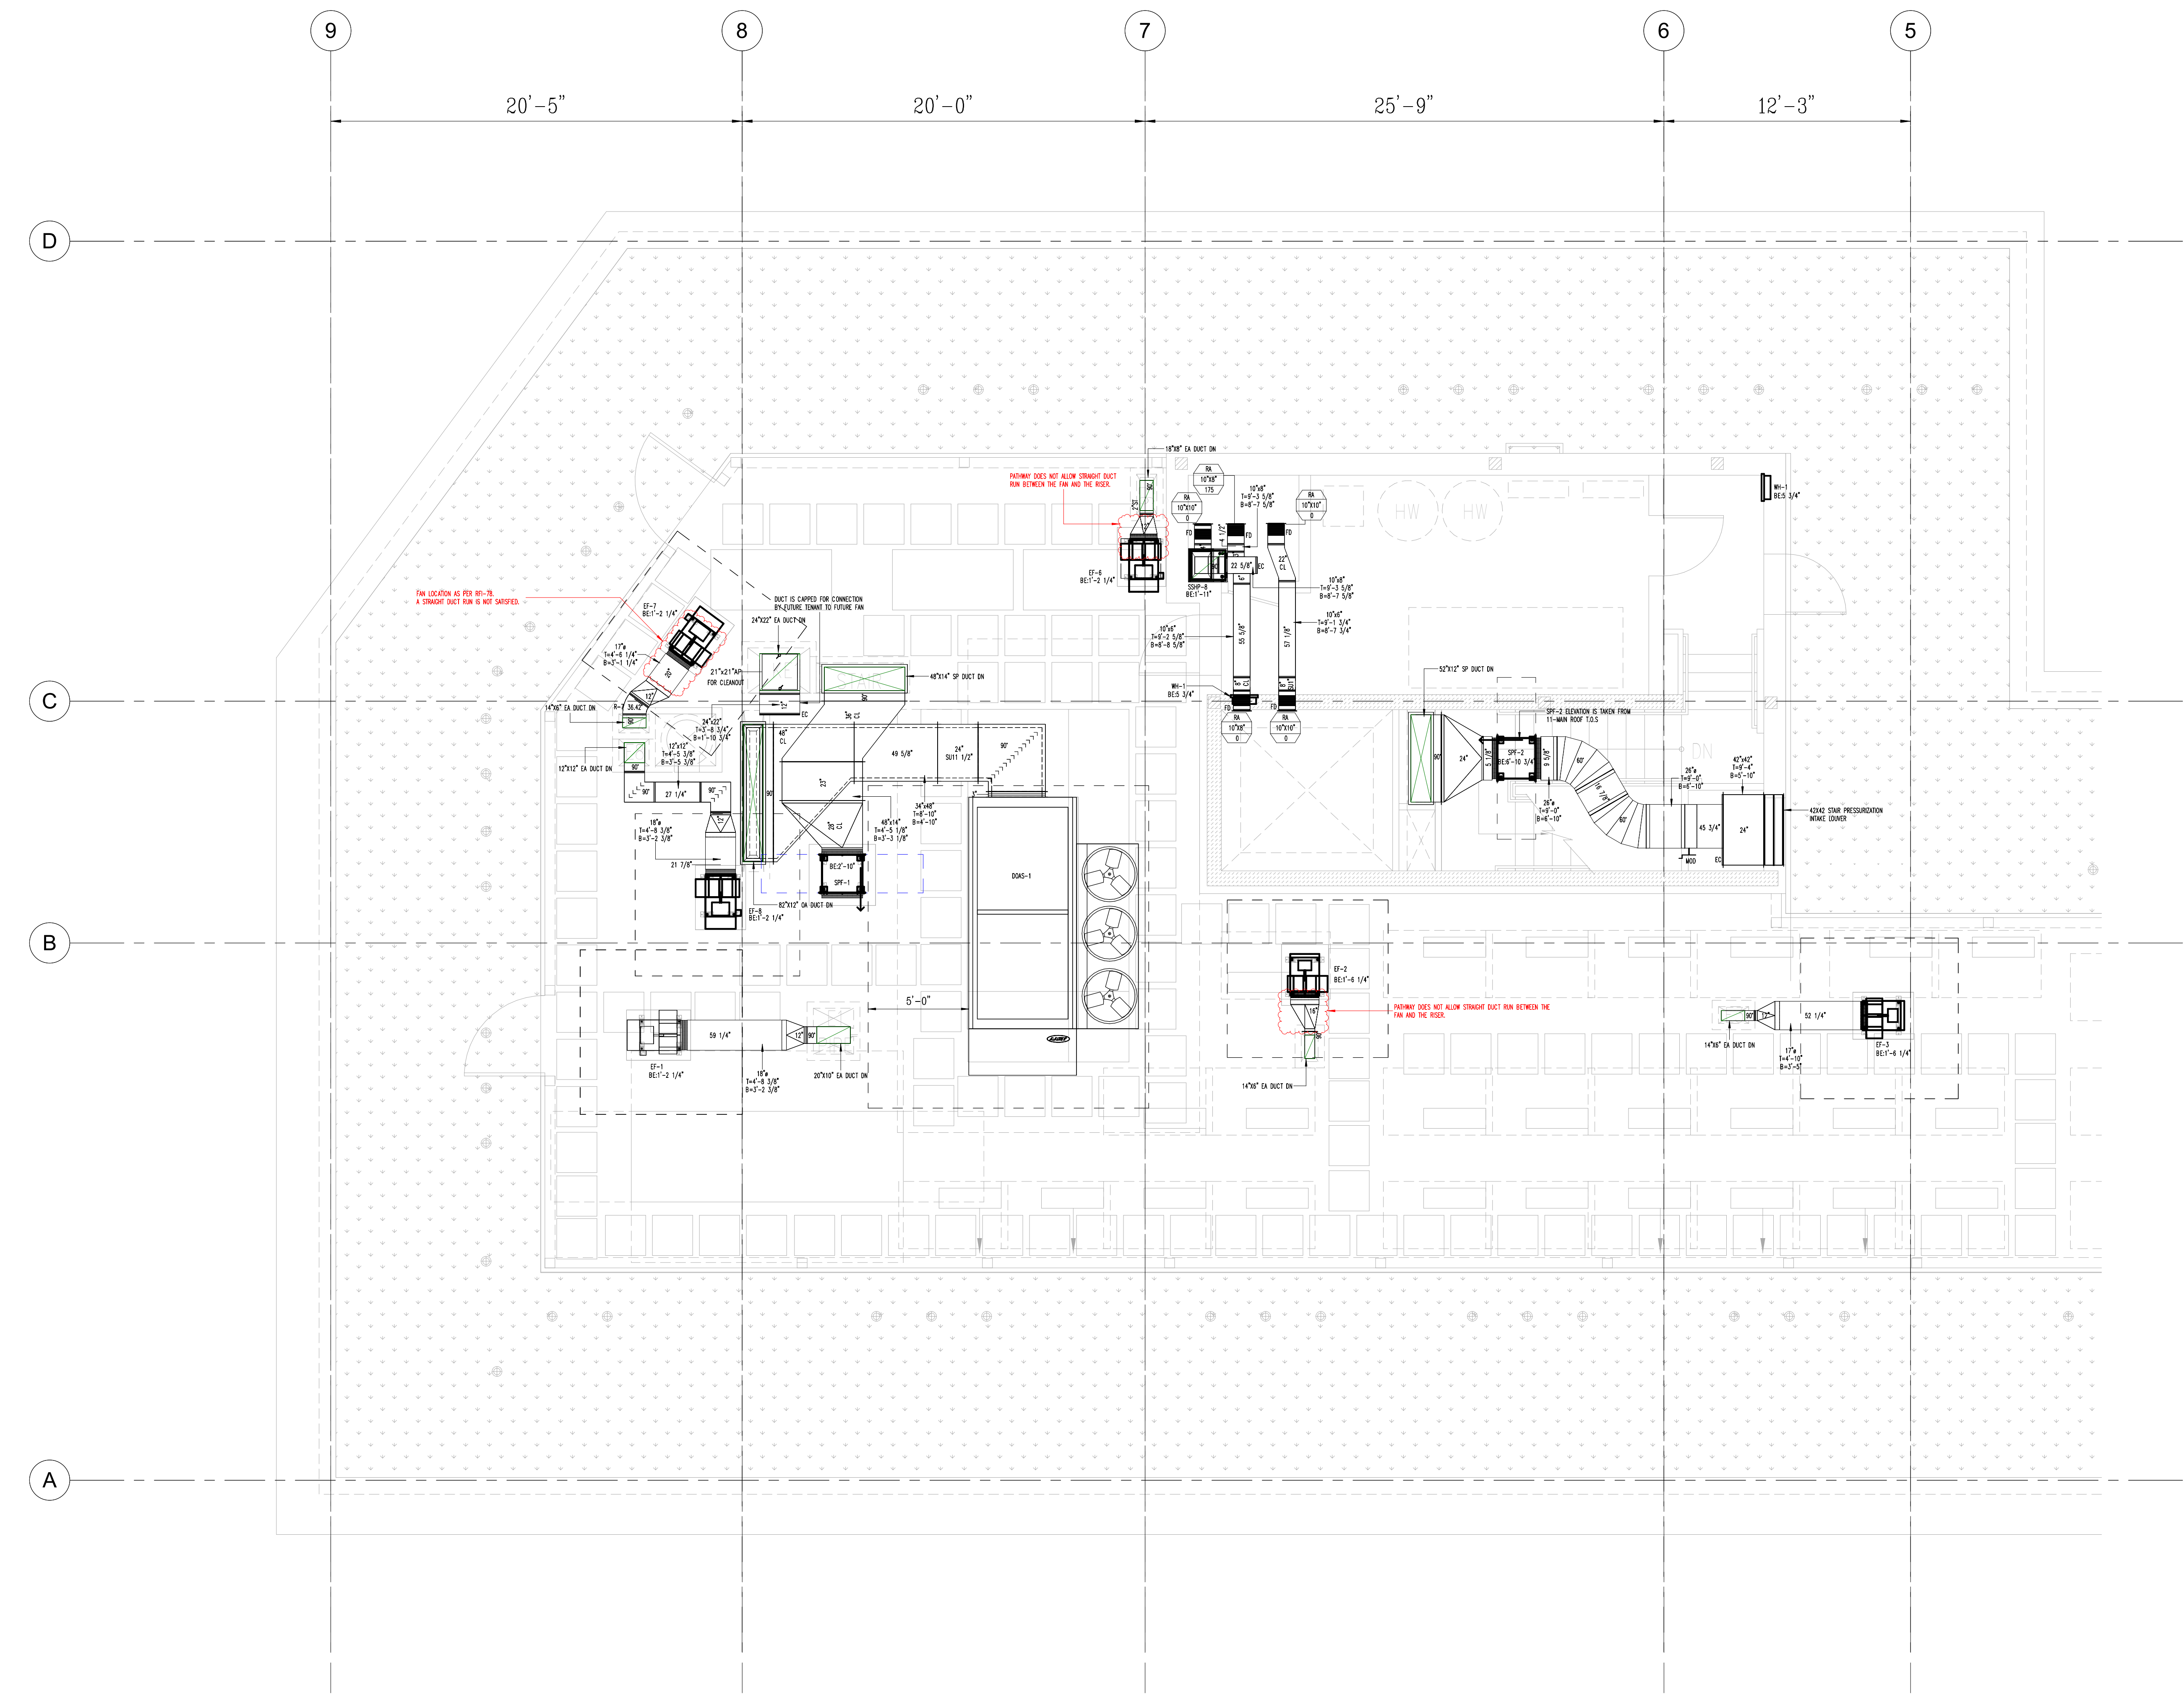

11-MAIN ROOF T.O.S.O.H - AREA B
1/4" = 1'-0"

GENERAL NOTES
ALL ELEVATIONS ARE TAKEN FROM LEVEL - MAIN ROOF TOS=139.35'
ALL MECHANICAL EQUIPMENT ELEVATIONS ARE TAKEN FROM FFL

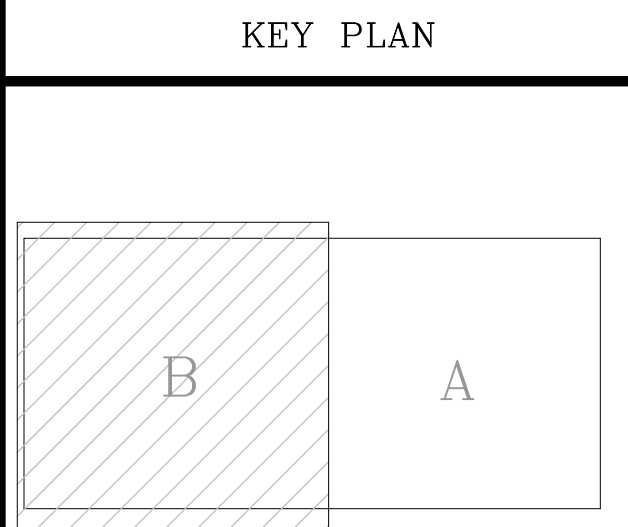


Updated as per comments	09/25/2025
For Review	08/06/2025
Revision/Issue	Date

Firm Name and Address

Project Name and Address
1109 CONGRESS STREET,NE
1009 CONGRESS STREET, NE
WASHINGTON, DC 20005

Project Area LEVEL- PH ROOF DUCT AREA B	Sheet SM-LPH-B-OH
Original Date 07/11/2025	Plot Date 09/25/2025
Scale 1/4"=1'-0"	

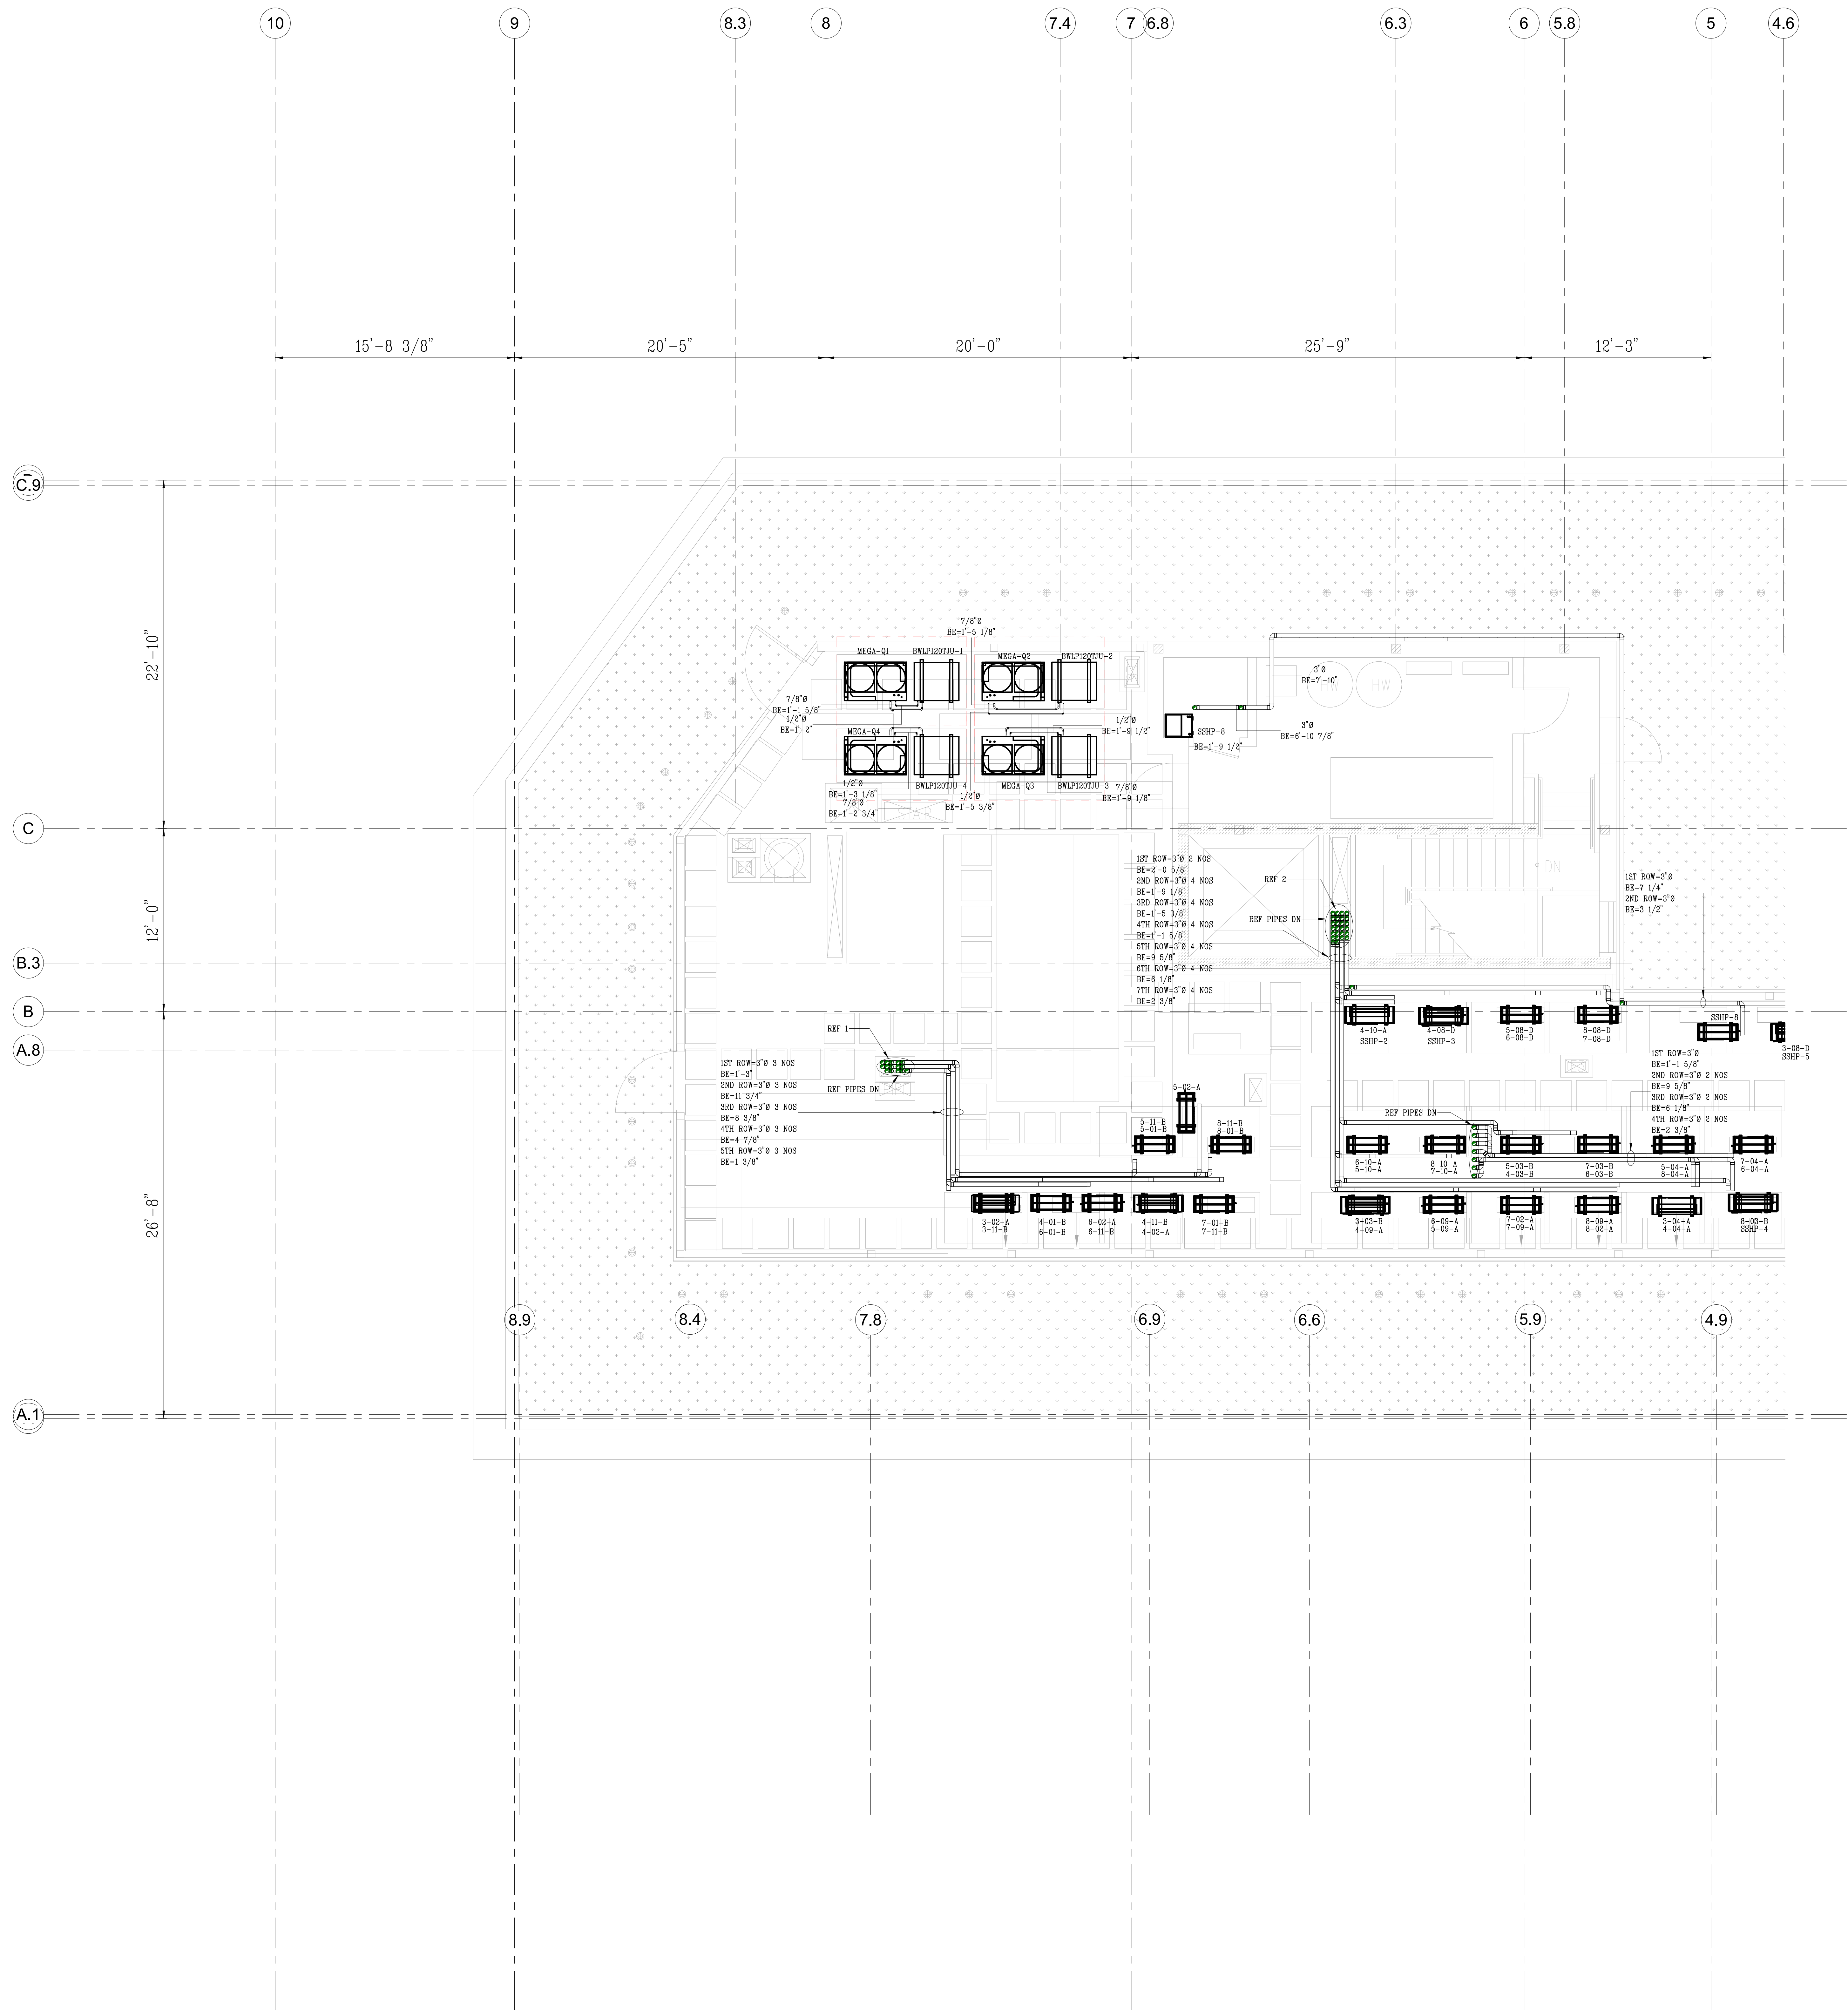

11-PENTHOUSE T.O.S. OH - AREA A
1/4" = 1'-0"

GENERAL NOTES

1. ALL ELEVATIONS ARE TAKEN FROM PENTHOUSE T.O.S. = 140.73'
2. ALL MECHANICAL EQUIPMENT BOTTOM ELEVATIONS ARE TAKEN FROM FINISH FLOOR LEVEL.

KEY PLAN

A

B

ABBREVIATIONS

5. Revision

09/26/2025

4. Revision

09/25/2025

3. Updated as per field Approve

08/06/2025

2. Revision

07/23/2025

1. For Approval

07/17/2025

Revision/Issue

Date

Firm Name and Address

Project Name and Address

1109 CONGRESS STREET
1109 CONGRESS STREET, NE
WASHINGTON, DC 20002

Project Area

MECHANICAL PIPING
OVERHEAD PLAN
PENTHOUSE AREA A

Original Date

07/17/2025

Plot Date

09/26/2025

Scale

1/4"=1'-0"

Sheet

MP_OH_PH-A

Firm Name and Address

Project Name and Address

1109 CONGRESS STREET
1109 CONGRESS STREET, NE
WASHINGTON, DC 20002

Project Area

MECHANICAL PIPING
OVERHEAD PLAN
PENTHOUSE AREA A

Original Date

07/17/2025

Plot Date


09/26/2025

Scale

1/4"=1'-0"

Sheet

MP_OH_PH-A

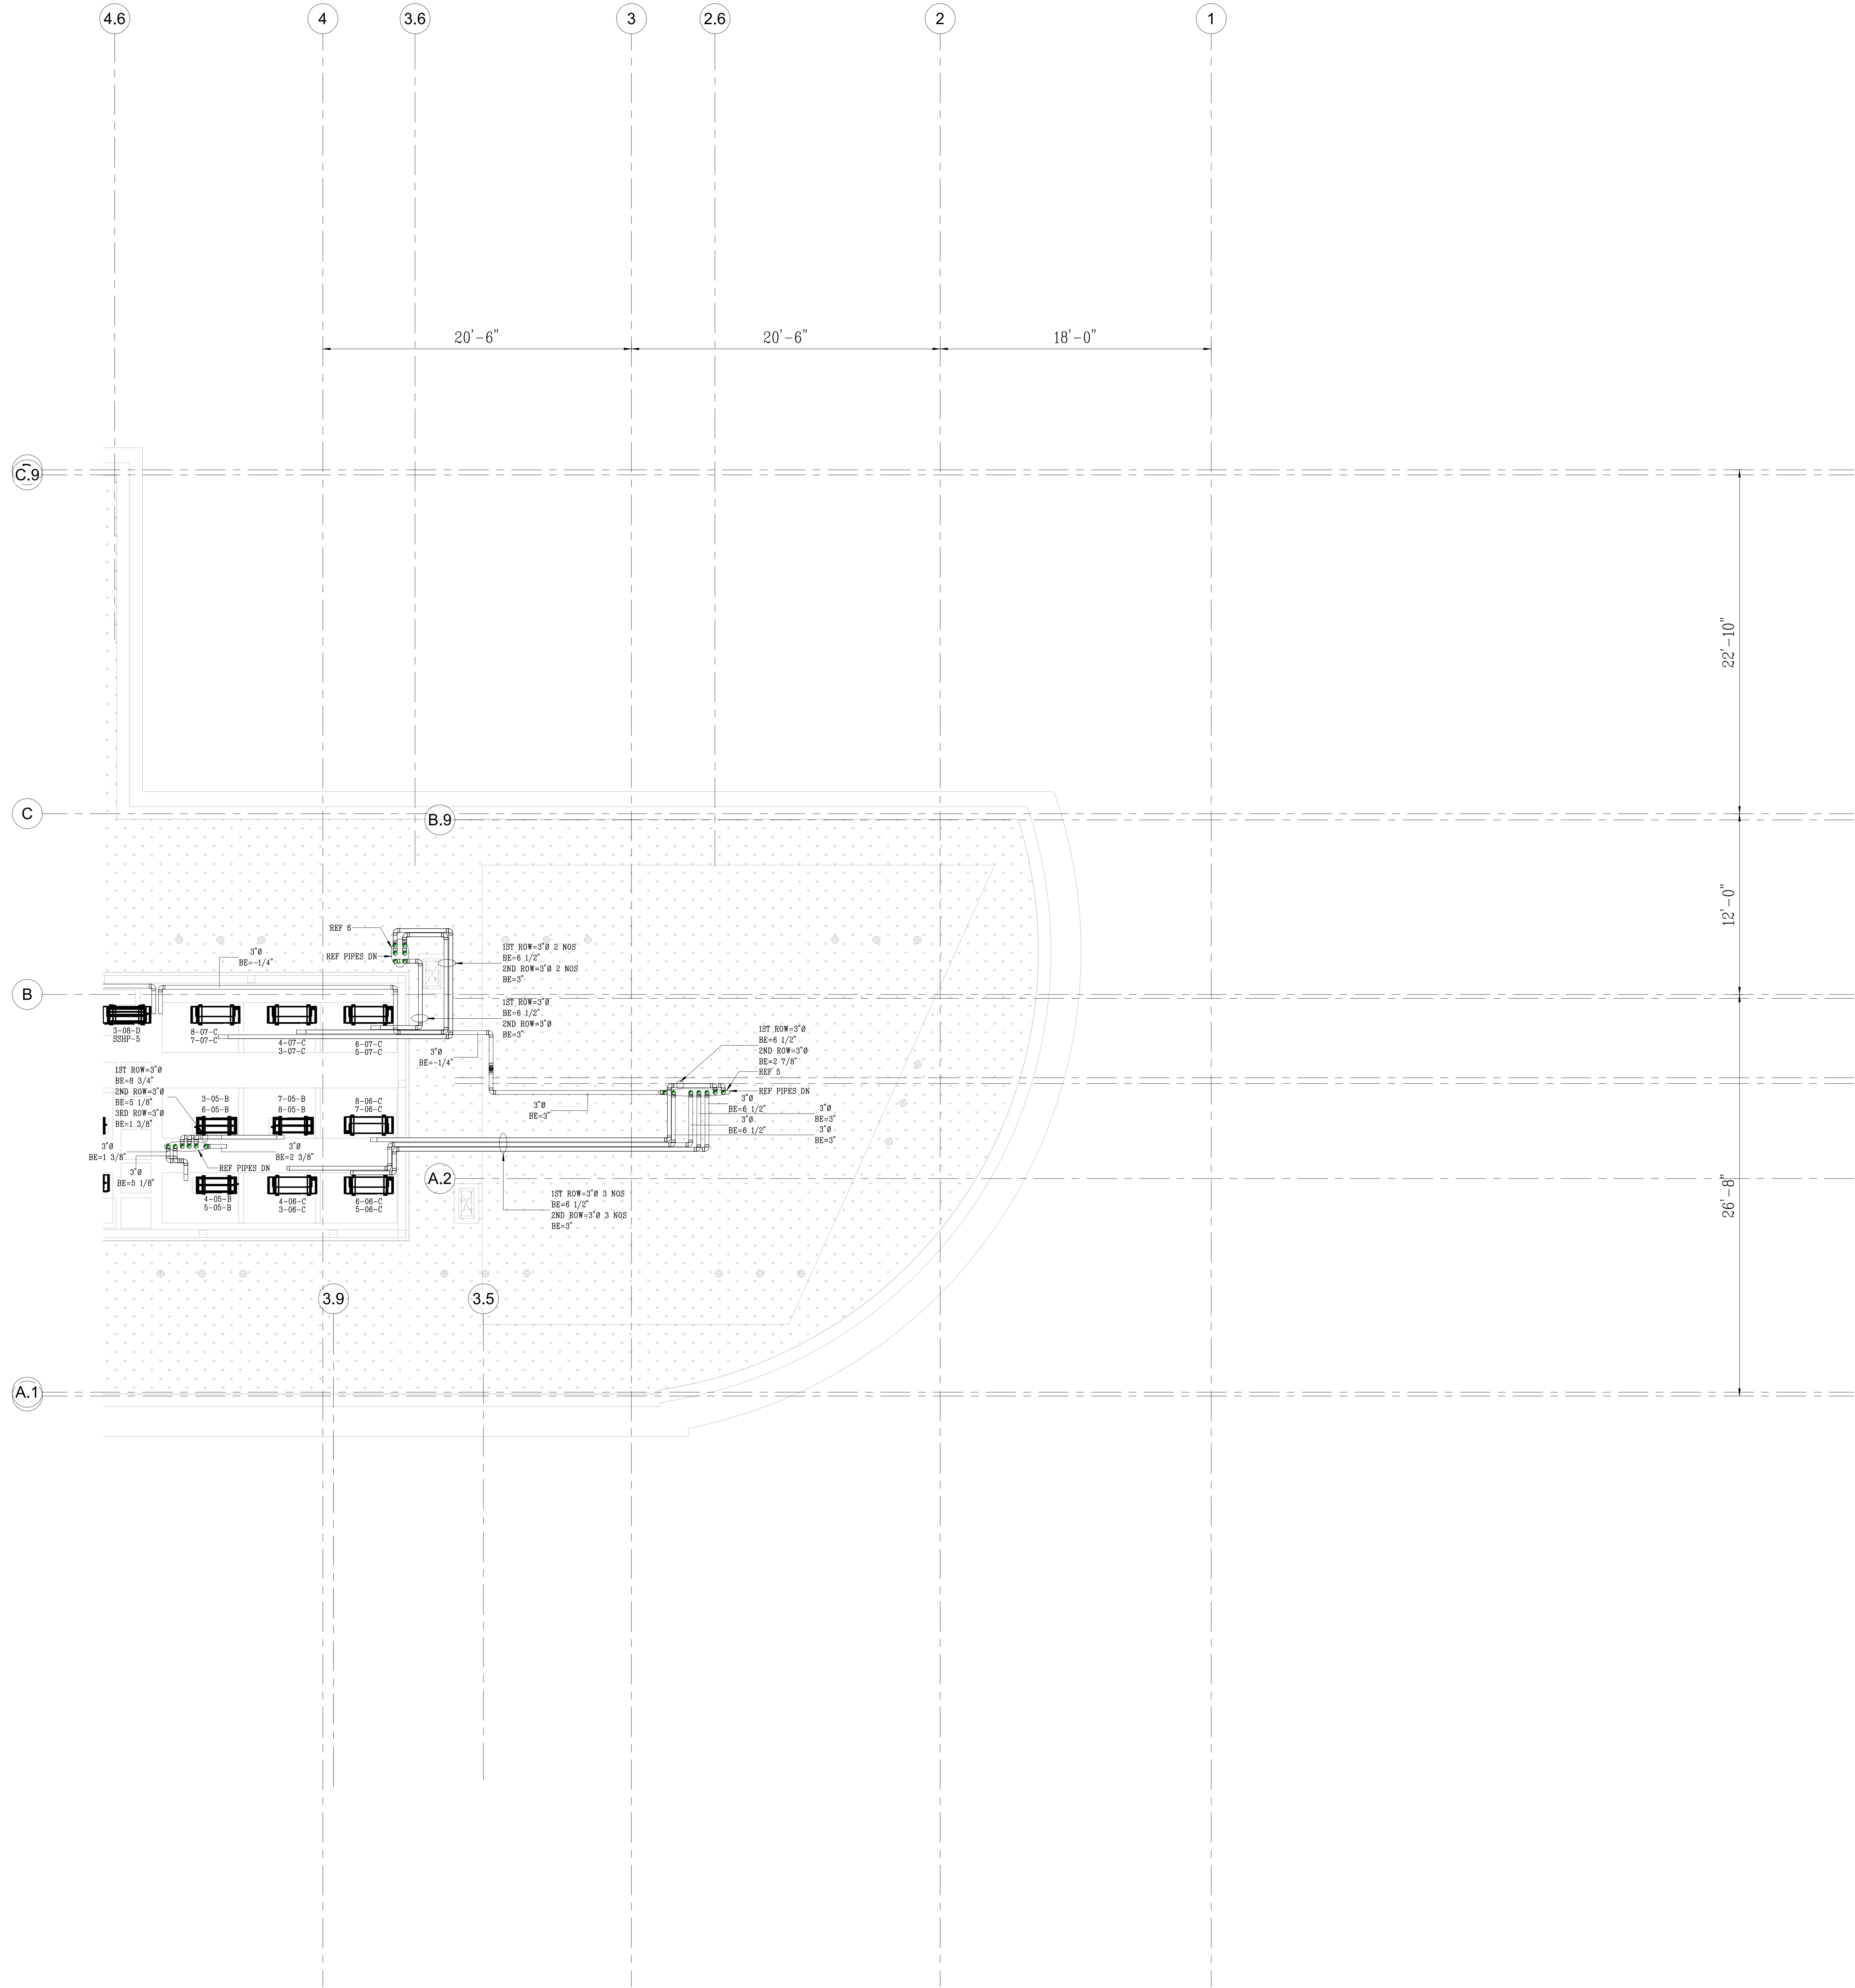


11-PENTHOUSE T.O.S. OH - AREA B
1/4" = 1'-0"

GENERAL NOTES

1. ALL ELEVATIONS ARE TAKEN FROM PENTHOUSE T.O.S. = 140.73'
2. ALL MECHANICAL EQUIPMENT BOTTOM ELEVATIONS ARE TAKEN FROM FINISH FLOOR LEVEL.

KEY PLAN

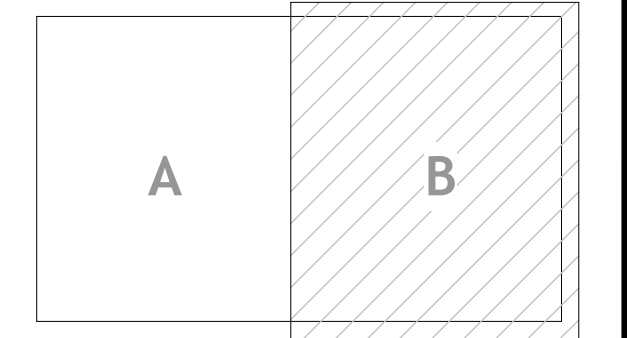

ABBREVIATIONS


5. Revision	09/26/2025
4. Revision	09/25/2025
3. Updated as per field Approve	08/06/2025
2. Revision	07/23/2025
1. For Approval	07/17/2025
Revision/Issue	Date

Firm Name and Address

Project Name and Address

1109 CONGRESS STREET
1109 CONGRESS STREET, NE
WASHINGTON, DC 20002


Project Area	Sheet
MECHANICAL PIPING OVERHEAD PLAN PENTHOUSE AREA B	MP_OH_PH-B
Original Date	Plot Date
07/17/2025	09/26/2025
Scale	1/4"=1'-0"

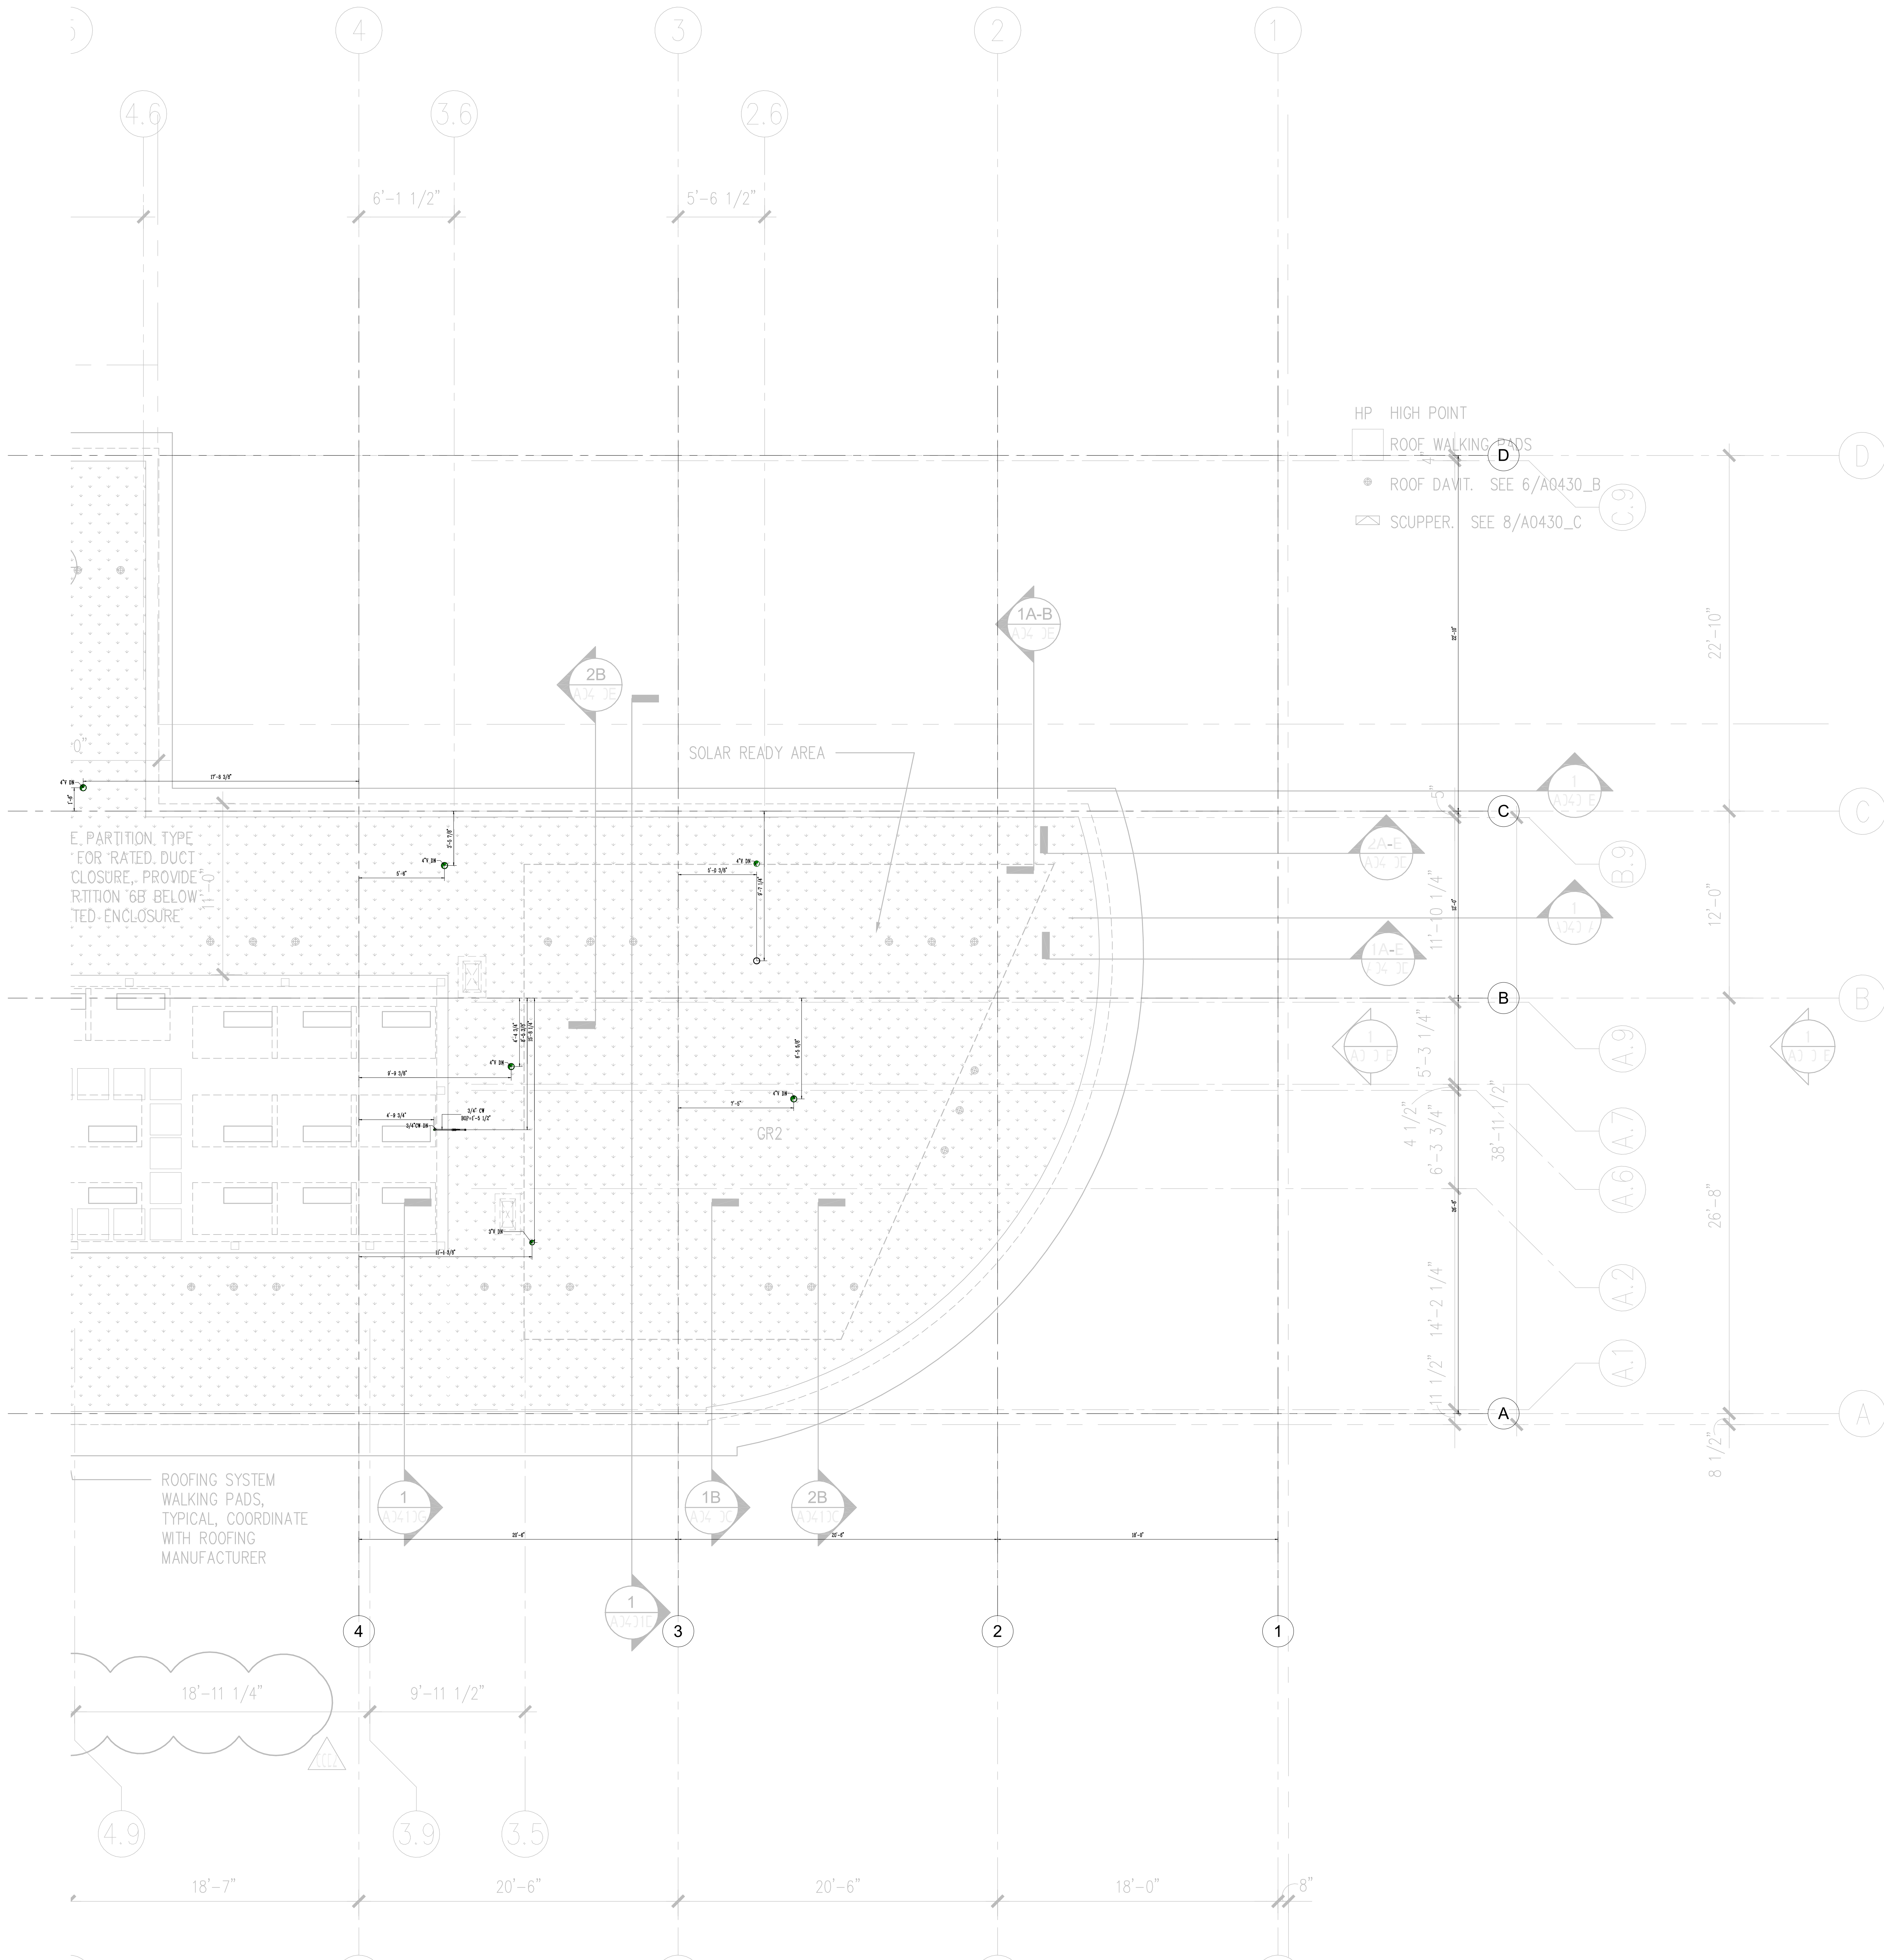

GENERAL NOTES

ALL ELEVATION ARE TAKEN FROM
BASE LINE ELEVATION OF LEVEL
PENTHOUSE(ROOF)=140.73'

KEY PLAN

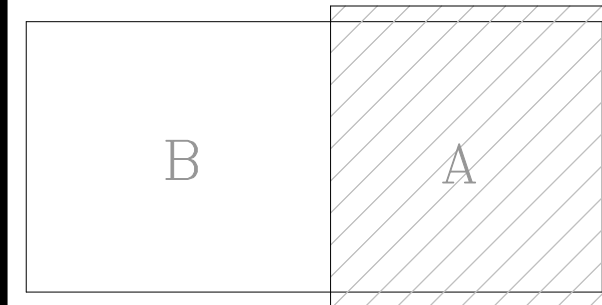

ABBREVIATIONS

PD-PUMP DISCHARGE
W-WASTE
SD-STORM DRAIN
V-VENT
SP- SUMP PUMP
SE-SEWAGE EJECTOR
B.T.-BOTTOM OF TANK
B.I.-BOTTOM OF INTERCEPTOR
FD-FLOOR DRAIN
FCO-FLOOR CLEANOUT
GD-GARAGE DRAIN
WSLV-WALL SLEEVE
BOP-BOTTOM OF PIPE
RD-ROOF DRAIN
OFD-OVERFLOW DRAIN
RL-RAINLEADER-STORM DRAIN
ORL-OVERFLOW RAINLEADER

1/ Revision-1 09/26/2025

UPDATE AS PER COMMENTS 09/24/2025 09/26/2025

FOR APPROVAL 08/13/2025

Revision/Issue Date

Firm Name and Address

Project Name and Address

1109 CONGRESS STREET

1109 CONGRESS STREET, NE
WASHINGTON, DC 20002

Project Area

LEVEL PH PLUMBING
AREA-A

Original Date Plot Date


08/13/2025 09/26/2025

Scale


1/4"=1'-0"

Sheet

PLM-LPH(ROOF)-A

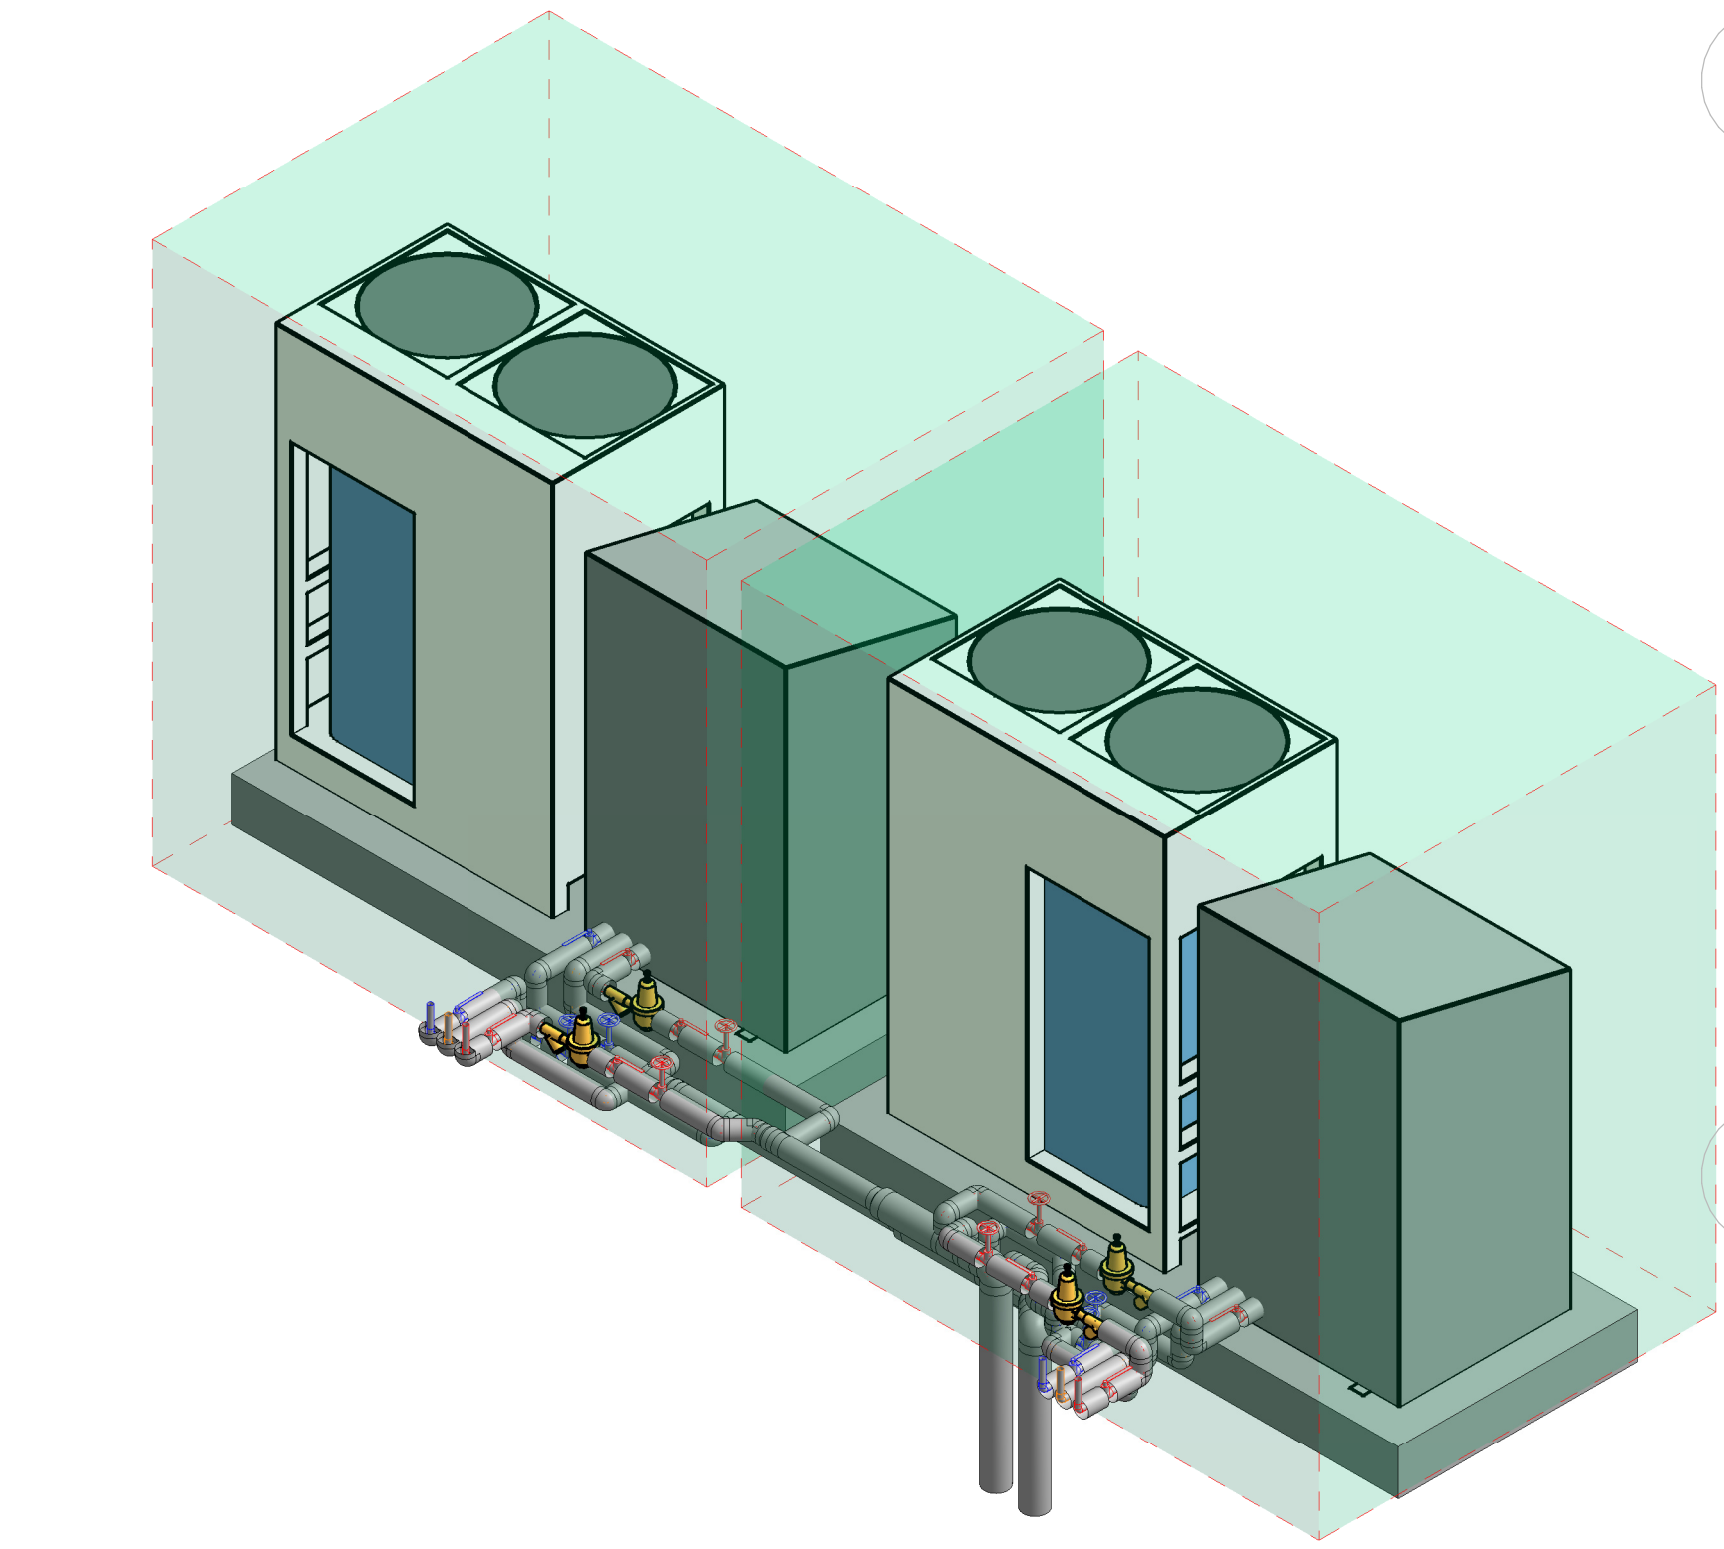

HPWH

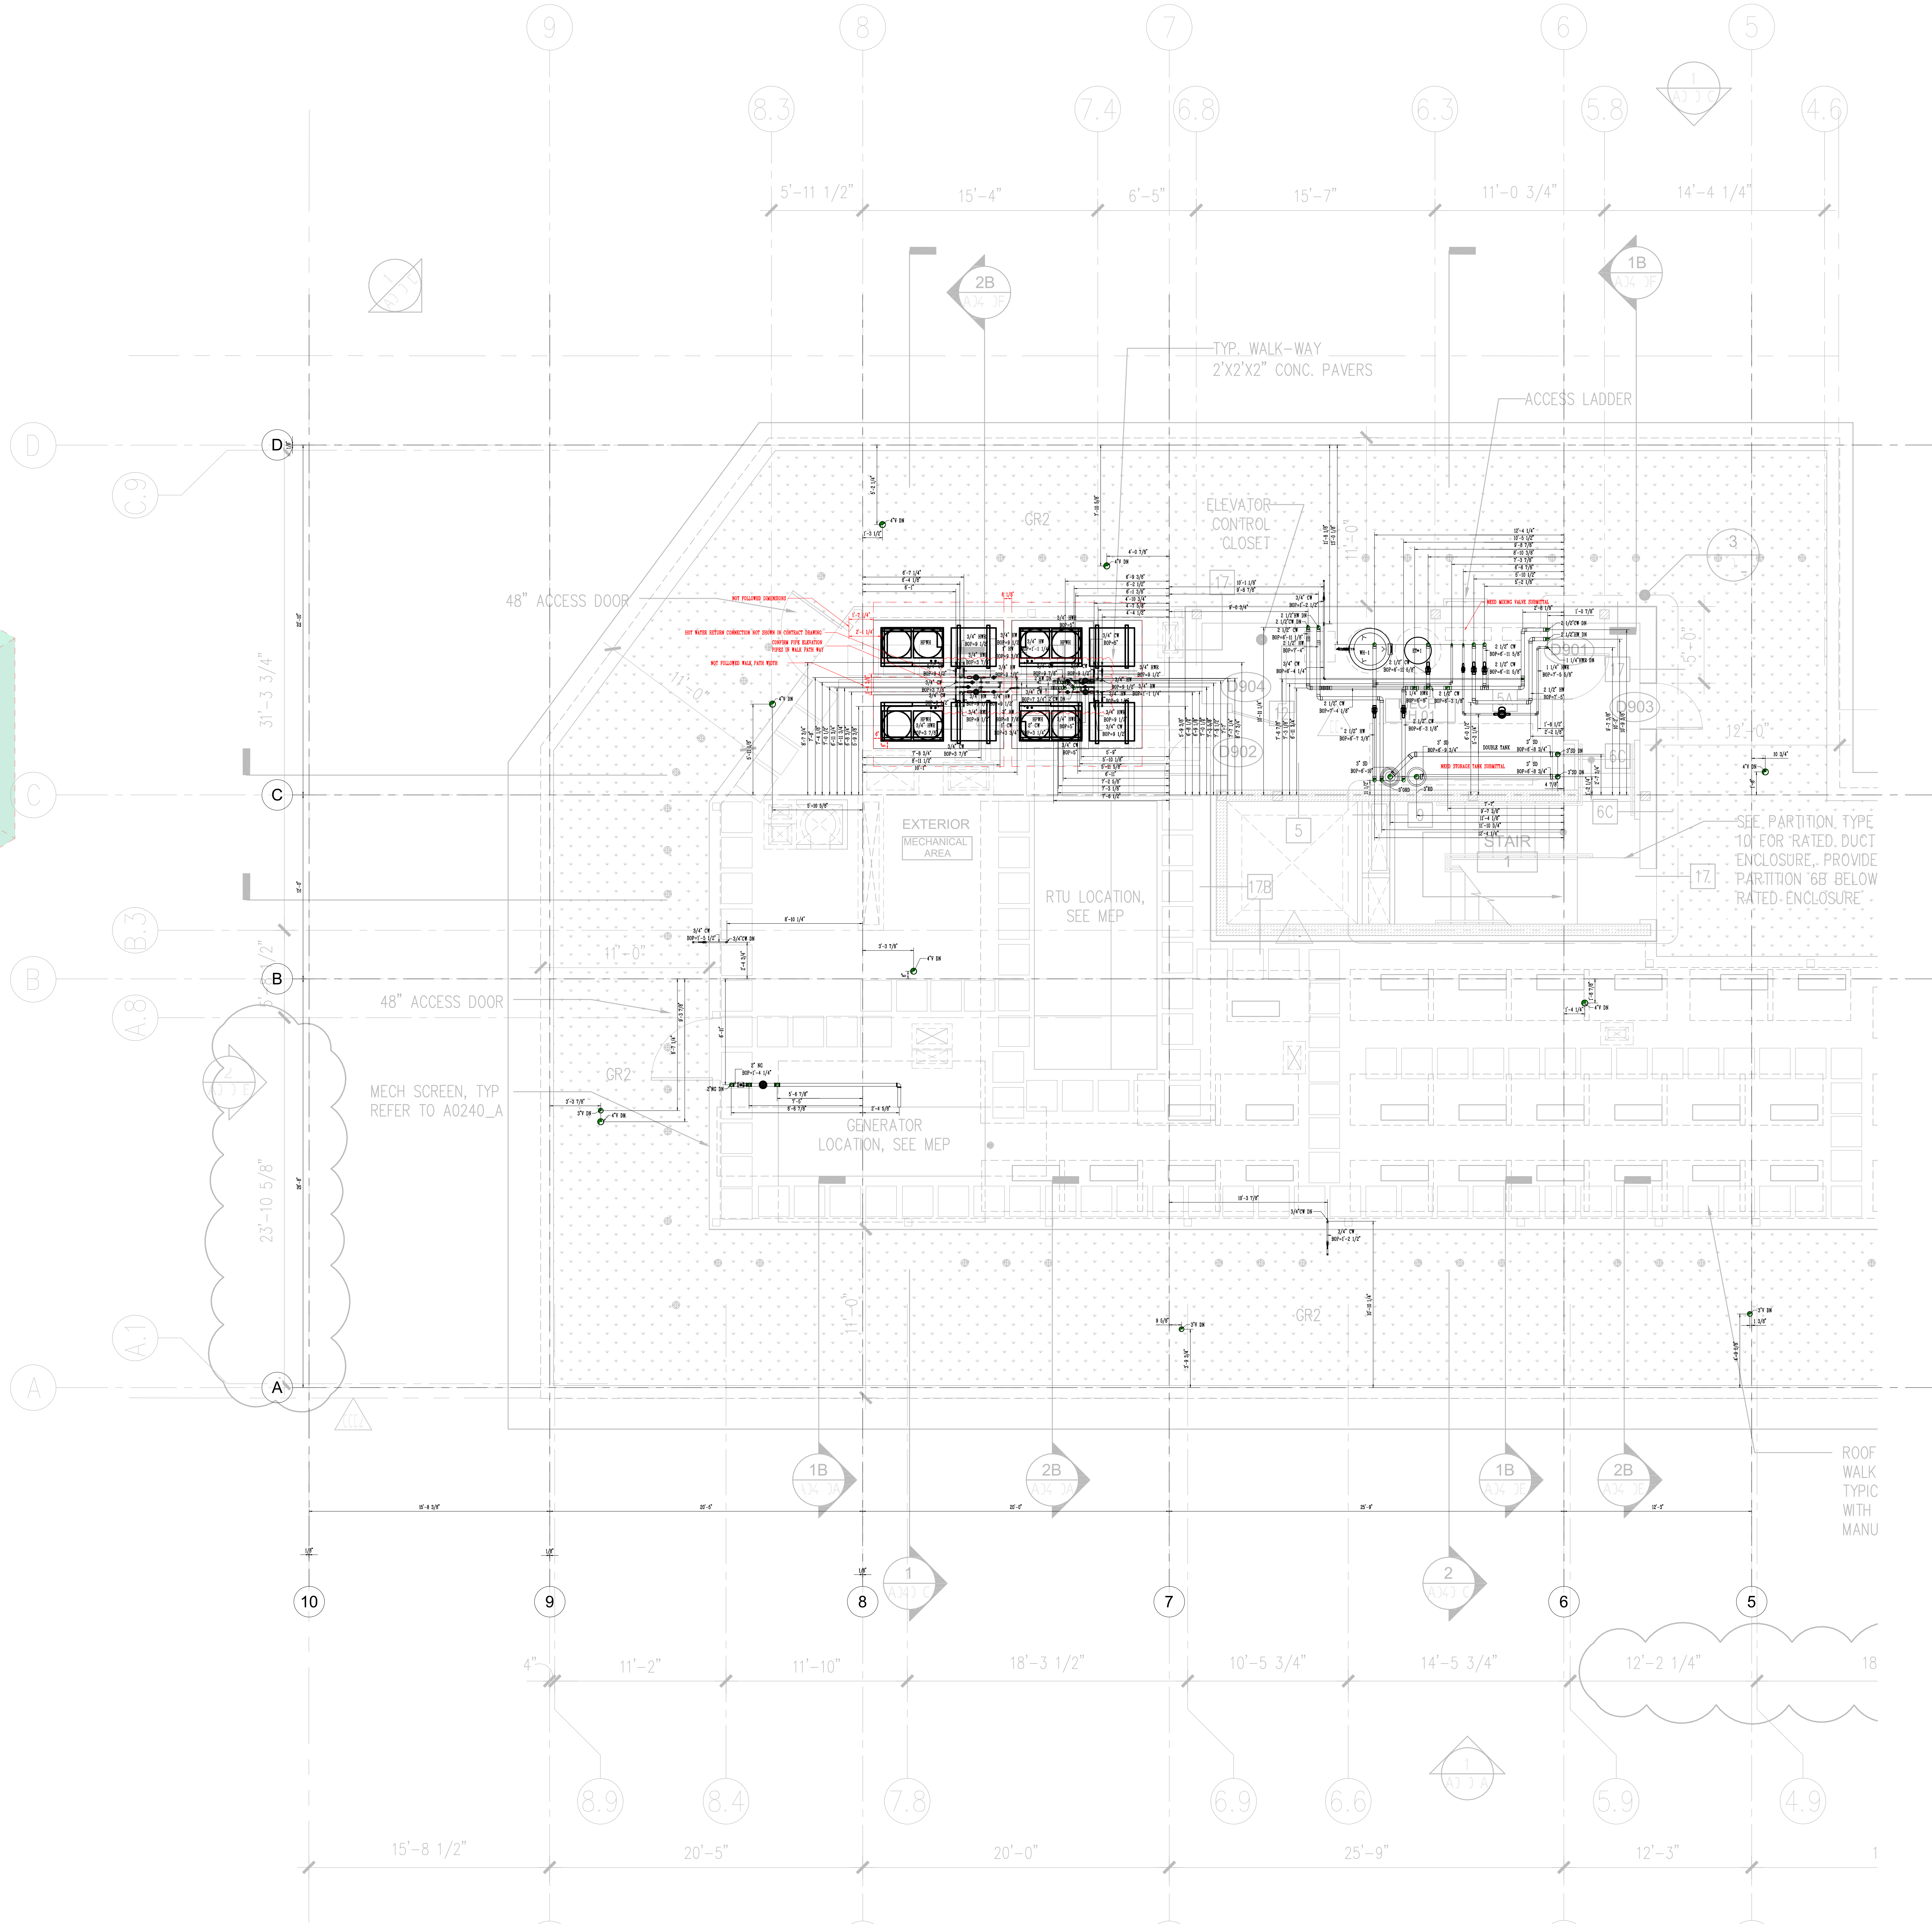

GENERAL NOTES

ALL ELEVATION ARE TAKEN FROM
BASE LINE ELEVATION OF LEVEL
PENTHOUSE(ROOF)=140.73'

KEY PLAN

ABBREVIATIONS

PD-PUMP DISCHARGE
W-WASTE
SD-STORM DRAIN
V-VENT
SP- SUMP PUMP
SE-SEWAGE EJECTOR
B.T.-BOTTOM OF TANK
B.I.-BOTTOM OF INTERCEPTOR
FD-FLOOR DRAIN
FCO-FLOOR CLEANOUT
GD-GARAGE DRAIN
WSLV-WALL SLEEVE
BOP-BOTTOM OF PIPE
RD-ROOF DRAIN
OPD-OVERFLOW DRAIN
RL-RAINLEADER-STORM DRAIN
ORL-OVERFLOW RAINLEADER

Revision

1	Revision-1	09/26/2025
2	UPDATE AS PER COMMENTS 09/24/2025	09/26/2025
3	FOR APPROVAL	09/26/2025
4	Revision/Issue	Date

Firm Name and Address

Project Name and Address

1109 CONGRESS STREET
WASHINGTON, DC 20005

Project Area

LEVEL PH PLUMBING
AREA-B

Sheet

PLB-LPH(ROOF)-B

Original Date

08/13/2025

Plot Date

09/26/2025

Scale

1/4\"/>